

M/S. B.S. ENGINEERING

Factory: Plot-09, N,S Road, Block-H,
Sector-2, Jahirul Islam City,
Aftabnagar, Dhaka-1212.

PROJECT NAME:

**STRUCTURAL DRAWING OF PROPOSED SINGLE-STORIED
STEEL BUILDING AT UTTARA, DHAKA.**

CLIENT : MR. JAHANGIR
REF. : BS-26-031
DATE : July 2026



REV.:	SCALE:	DWG.NO.
00	NTS	ST-01

REV.:	SCALE:	DWG.NO.
00	NTS	ST-01



Factory: Plot-09, N,S Road,
Block-H, Sector-2,
Jahirul Islam City,
Aftabnagar, Dhaka-1212.

PROPOSED SINGLE-STORIED
PRE-FABRICATED STEEL
BUILDING.

MR. JAHANGIR

BS-26-031

MD. REJAUL KARIM
B.Sc. ENGINEER (CIVIL), MIEB


MD. RIFAT MAHMUD SAJIB
B.Sc. ENGINEER (CIVIL), MIEB

Polash

STEEL COLUMN LAYOUT PLAN

23.07.2026

REV.:	SCALE:	DWG.NO.
00	NTS	ST-02

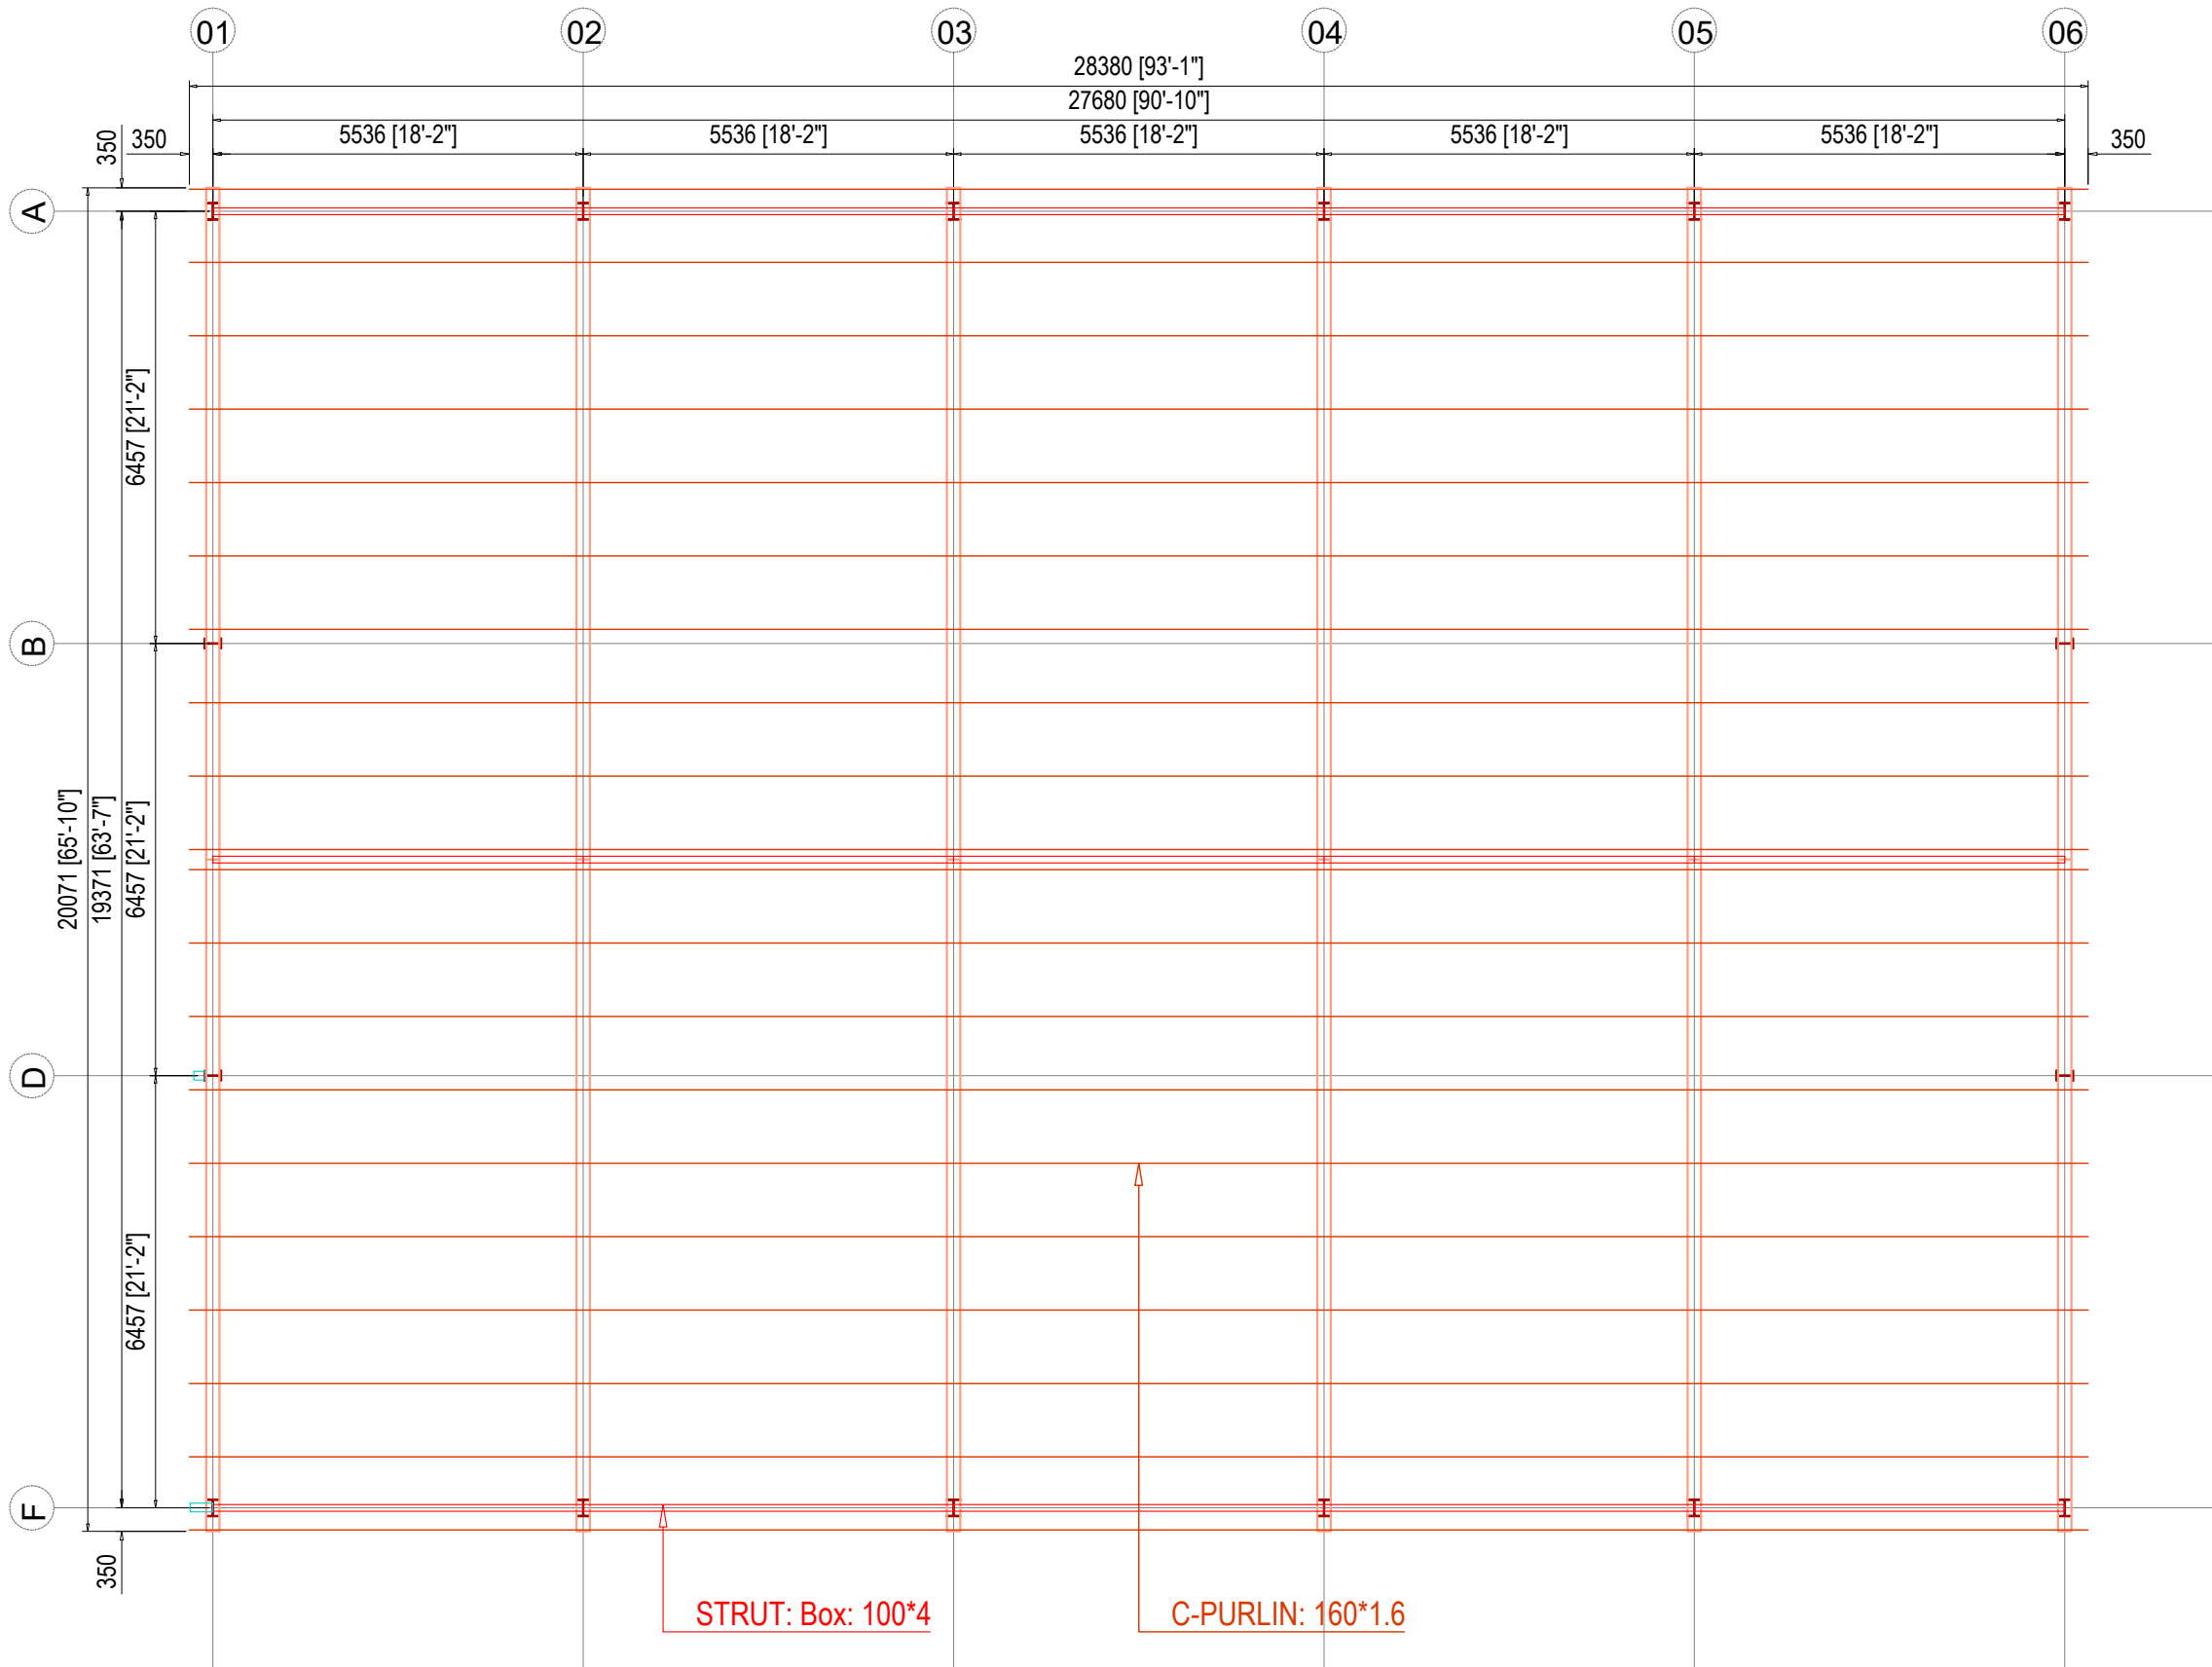

ROOF STEEL FRAMING (RAFTER, STRUT MEMBER) LAYOUT PLAN

M/S. B.S. ENGINEERING
Factory: Plot-09, N,S Road,
Block-H, Sector-2,
Jahirul Islam City,
Aftabnagar, Dhaka-1212.

PROJECT:
PROPOSED SINGLE-STORIED
PRE-FABRICATED STEEL
BUILDING.

CLIENT:
MR. JAHANGIR

REFERENCE NO.:
BS-26-031

DESIGNER:

MD. REJAUL KARIM
B.Sc. ENGINEER (CIVIL), MIEB

MD. RIFAT MAHMUD SAJIB
B.Sc. ENGINEER (CIVIL), MIEB

DRAWN BY:
Polash

DRAWING TITLE:
ROOF STEEL FRAMING (RAFTER,
STRUT MEMBER) LAYOUT PLAN

DATE:
23.07.2026

REV.:	SCALE:	DWG.NO.
00	NTS	ST-04



M/S. B.S. ENGINEERING
Factory: Plot-09, N,S Road,
 Block-H, Sector-2,
 Jahirul Islam City,
 Aftabnagar, Dhaka-1212.

PROJECT:

PROPOSED SINGLE-STORIED
PRE-FABRICATED STEEL
BUILDING.

CLIENT:

MR. JAHANGIR

REFERENCE NO.:
BS-26-031

DESIGNER:

MD. REJAUL KARIM
B.Sc. ENGINEER (CIVIL), MIEB

MD. RIFAT MAHMUD SAJIB
B.Sc. ENGINEER (CIVIL), MIEB

DRAWN BY:


Polash

DRAWING TITLE:

ROOFING LAYOUT PLAN

DATE:
23.07.2026

REV.:	SCALE:	DWG.NO.
00	NTS	ST-06

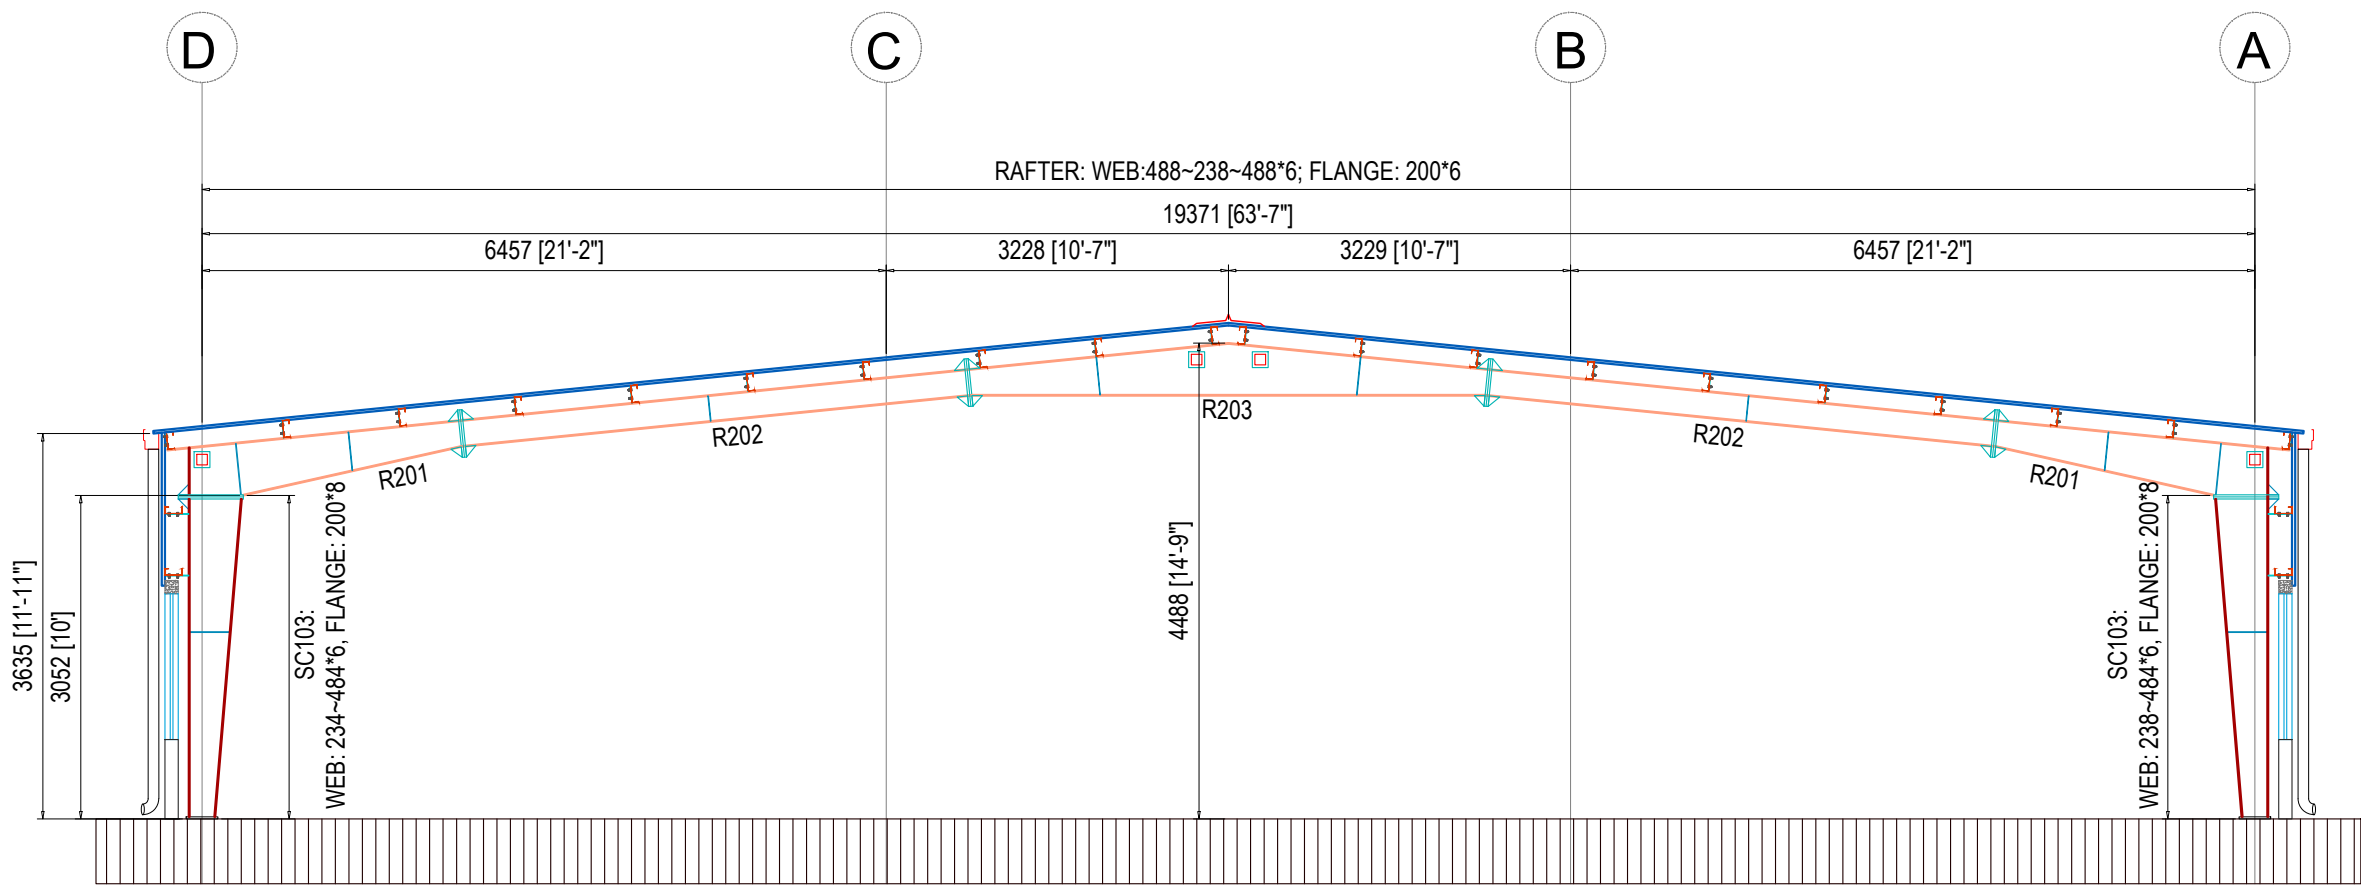

SECTION : 02~05

CROSS SECTION OF GRID: 02~05

M/S. B.S. ENGINEERING
Factory: Plot-09, N,S Road,
Block-H, Sector-2,
Jahirul Islam City,
Aftabnagar, Dhaka-1212.

PROJECT:
PROPOSED SINGLE-STORIED
PRE-FABRICATED STEEL
BUILDING.

CLIENT:
MR. JAHANGIR

REFERENCE NO.:
BS-26-031

DESIGNER:

MD. REJAUL KARIM
B.Sc. ENGINEER (CIVIL), MIEB

MD. RIFAT MAHMUD SAJIB
B.Sc. ENGINEER (CIVIL), MIEB

DRAWN BY:
Polash

DRAWING TITLE:
CROSS SECTION OF GRID:
02~05

DATE:
23.07.2026

REV.:	SCALE:	DWG.NO.
00	NTS	ST-09

M/S. B.S. ENGINEERING
Factory: Plot-09, N,S Road,
Block-H, Sector-2,
Jahirul Islam City,
Aftabnagar, Dhaka-1212.

PROJECT:
PROPOSED SINGLE-STORIED
PRE-FABRICATED STEEL
BUILDING.

CLIENT:
MR. JAHANGIR

REFERENCE NO.:
BS-26-031

DESIGNER:

MD. REJAUL KARIM
B.Sc. ENGINEER (CIVIL), MIEB


MD. RIFAT MAHMUD SAJIB
B.Sc. ENGINEER (CIVIL), MIEB






DRAWN BY:
Polash

DRAWING TITLE:
CROSS SECTION OF GRID 01 &
06

DATE:
23.07.2026

REV.:	SCALE:	DWG.NO.
00	NTS	ST-09

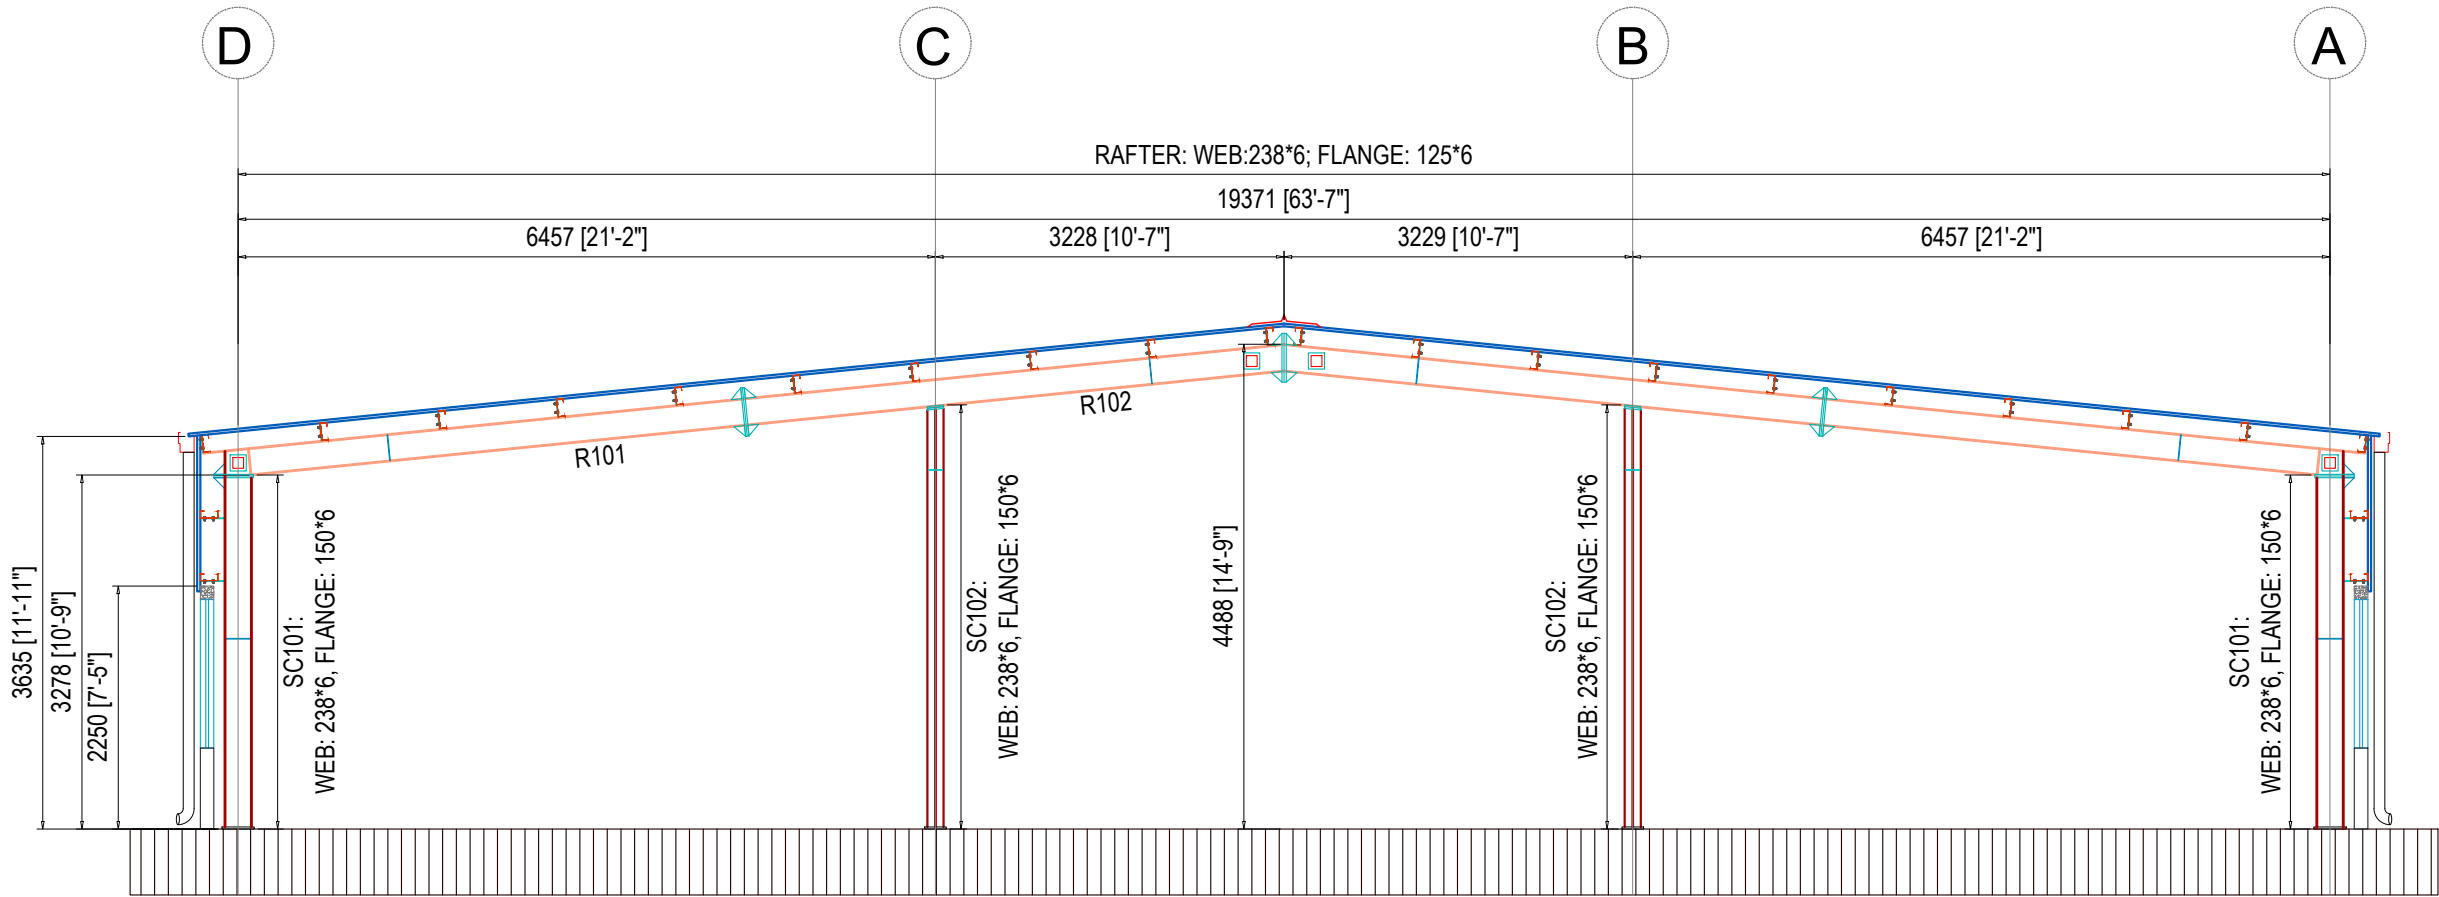

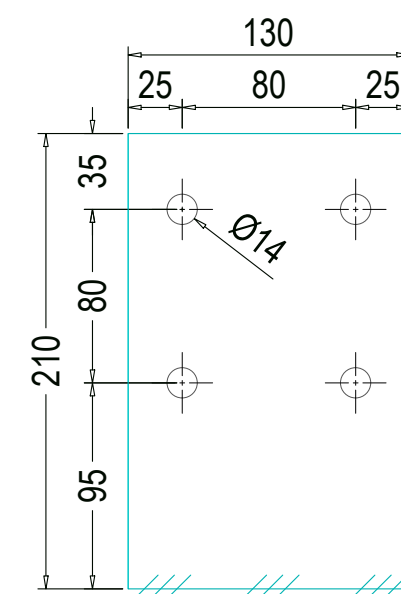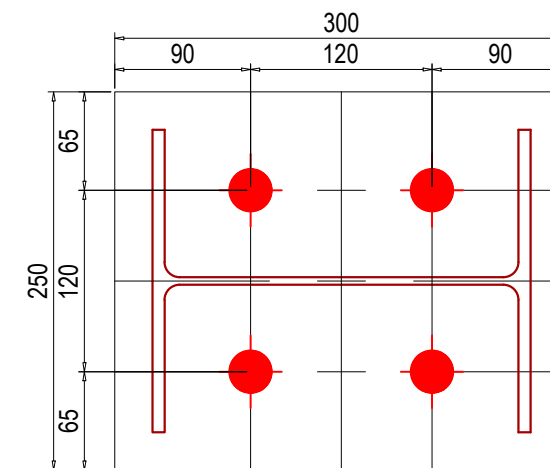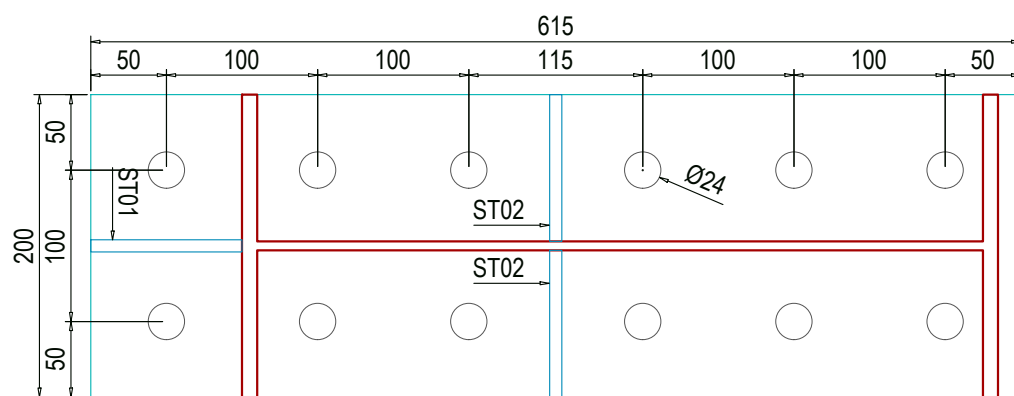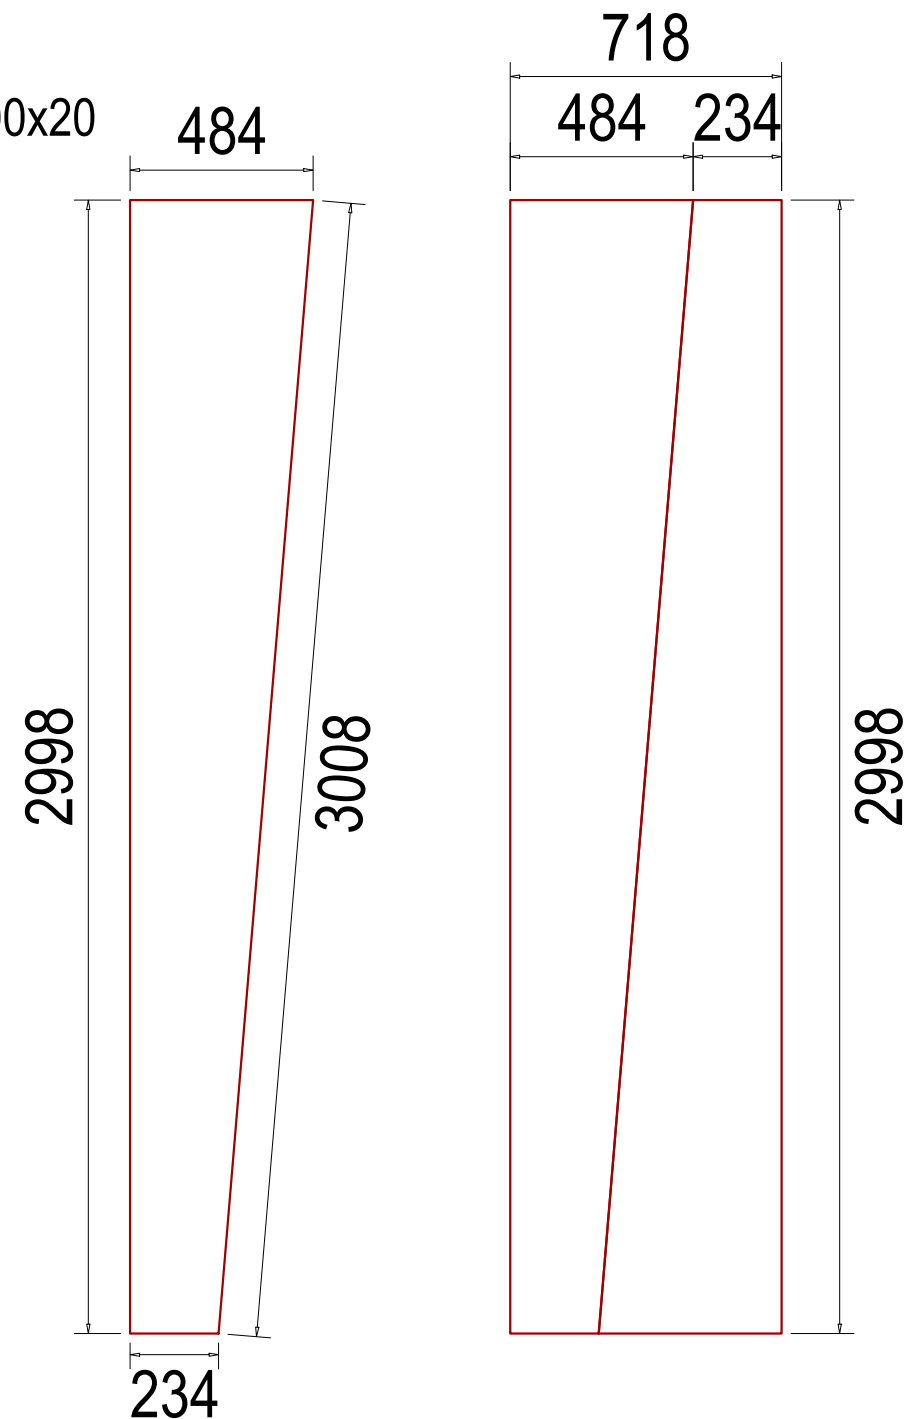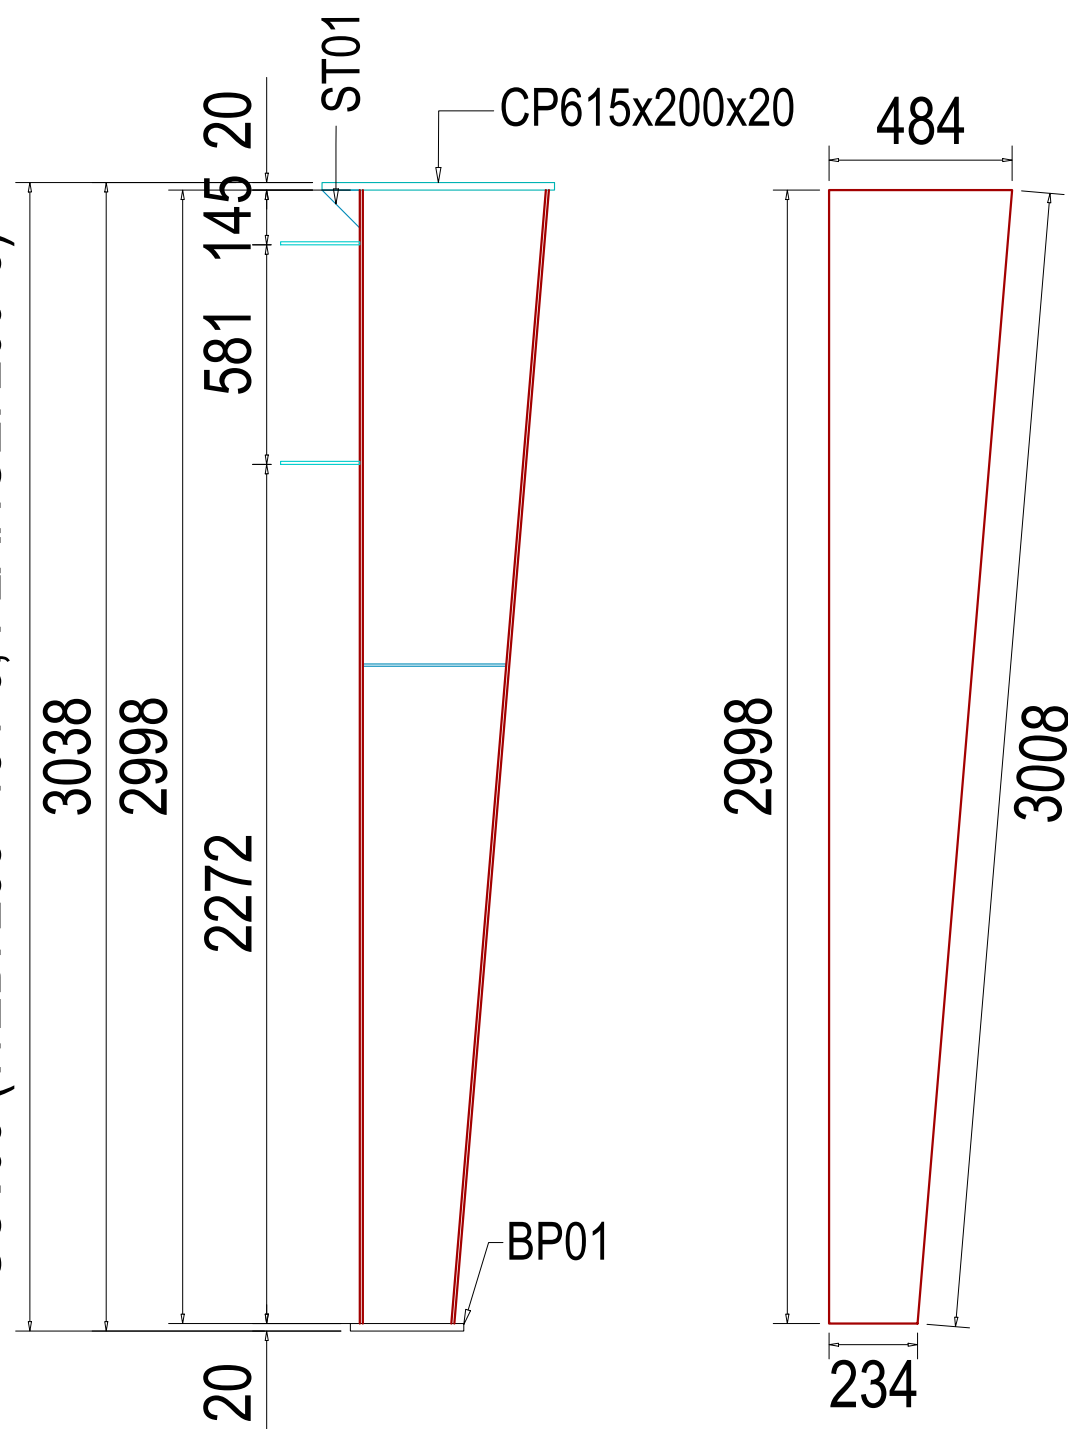

M/S. B.S. ENGINEERING

Factory: Plot-09, N,S Road,
Block-H, Sector-2,
Jahirul Islam City,
Aftabnagar, Dhaka-1212.

PROJECT:

PROPOSED SINGLE-STORIED
PRE-FABRICATED STEEL
BUILDING.

CLIENT:

MR. JAHANGIR

REFERENCE NO.:

BS-26-031

DESIGNER:

MD. REJAUL KARIM
B.Sc. ENGINEER (CIVIL), MIEB

MD. RIFAT MAHMUD SAJIB
B.Sc. ENGINEER (CIVIL), MIEB

DRAWN BY:

Polash

DRAWING TITLE:

DETAIL OF SC03

DATE:

23.07.2026

REV.:

00


SCALE:

NTS

DWG.NO.


ST-10

SC101 (WEB: 238*6; FLANGE: 125*6)

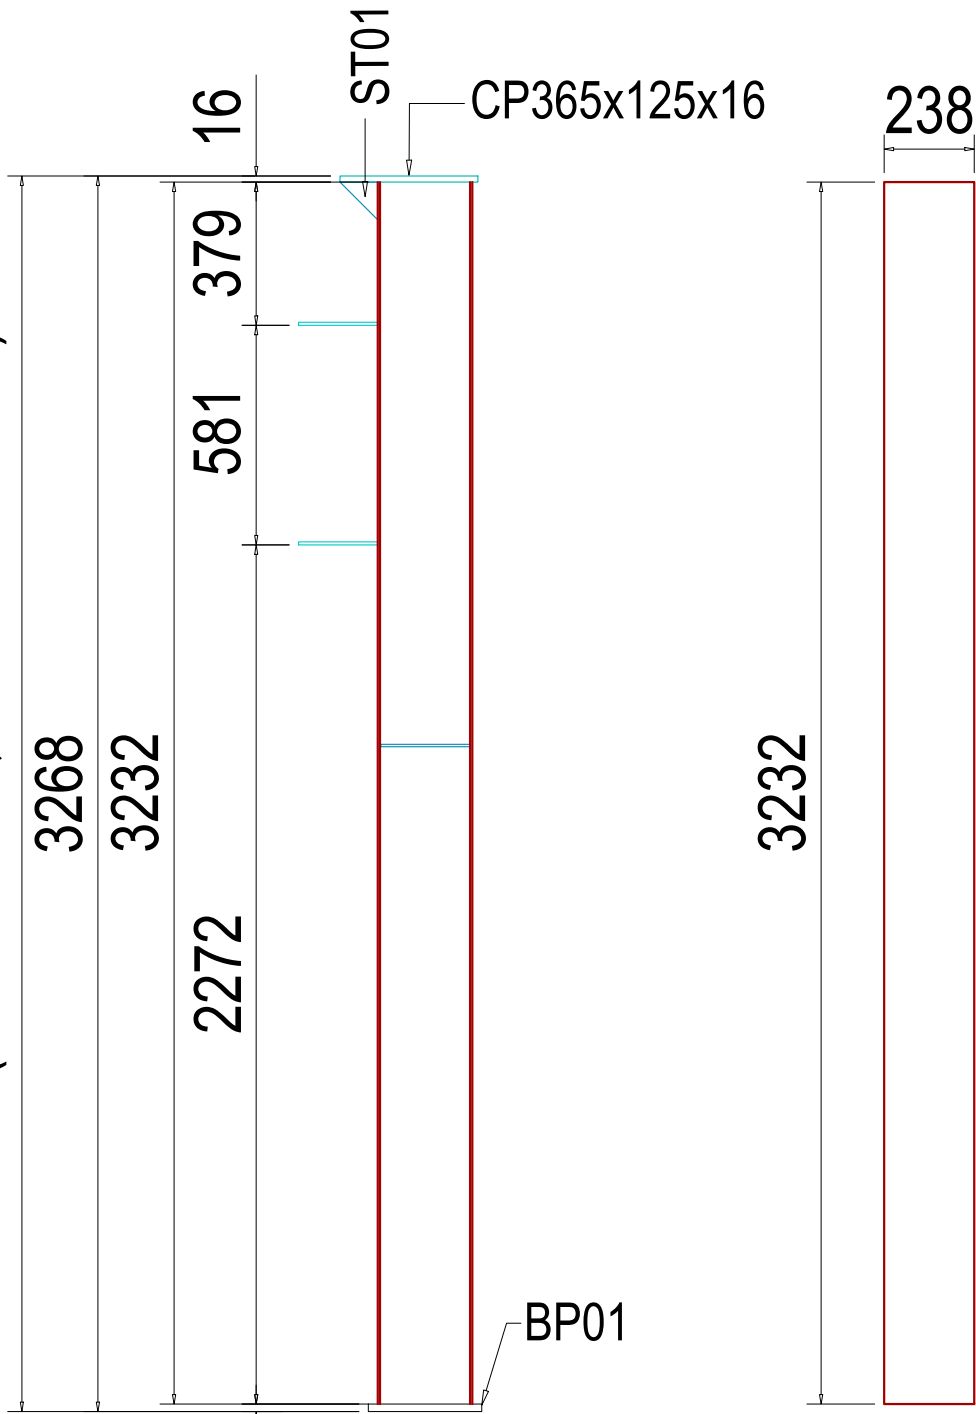


DETAIL OF SC101
(04 PCS)


CUTTING WEB OF SC01

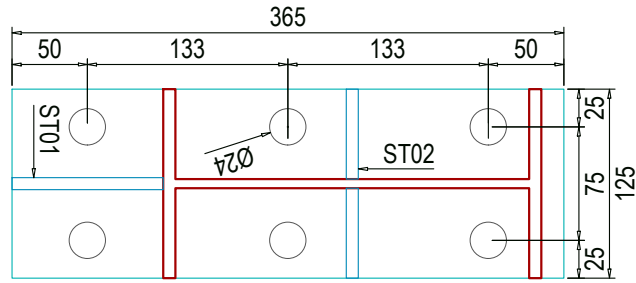

DETAILS OF CP365x125x16
(16mm Thickness)
Qty: 08Nos

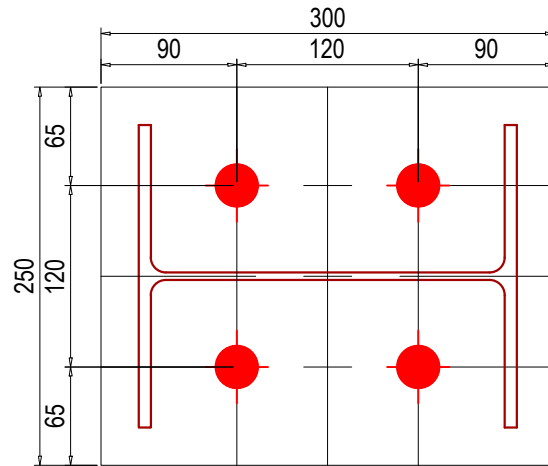

DETAILS OF BP01
(THICK: 20mm);Total: 16Nos.

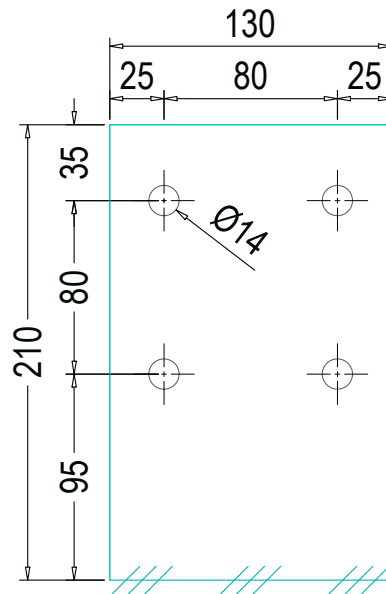

DETAILS OF PC210*6
(THICKNESS 6mm)
Qty: 24Nos

M/S. B.S. ENGINEERING
Factory: Plot-09, N,S Road,
Block-H, Sector-2,
Jahirul Islam City,
Aftabnagar, Dhaka-1212.

PROJECT:
PROPOSED SINGLE-STORIED
PRE-FABRICATED STEEL
BUILDING.

CLIENT:
MR. JAHANGIR

REFERENCE NO.:
BS-26-031

DESIGNER:

MD. REJAUL KARIM
B.Sc. ENGINEER (CIVIL), MIEB

MD. RIFAT MAHMUD SAJIB
B.Sc. ENGINEER (CIVIL), MIEB

DRAWN BY:
Polash

DRAWING TITLE:
DETAIL SC101


DATE:
23.07.2026

REV.:	SCALE:	DWG.NO.
00	NTS	ST-11


SC102 (WEB: 238*6; FLANGE: 125*6)




DETAIL OF SC102
(04 PCS)

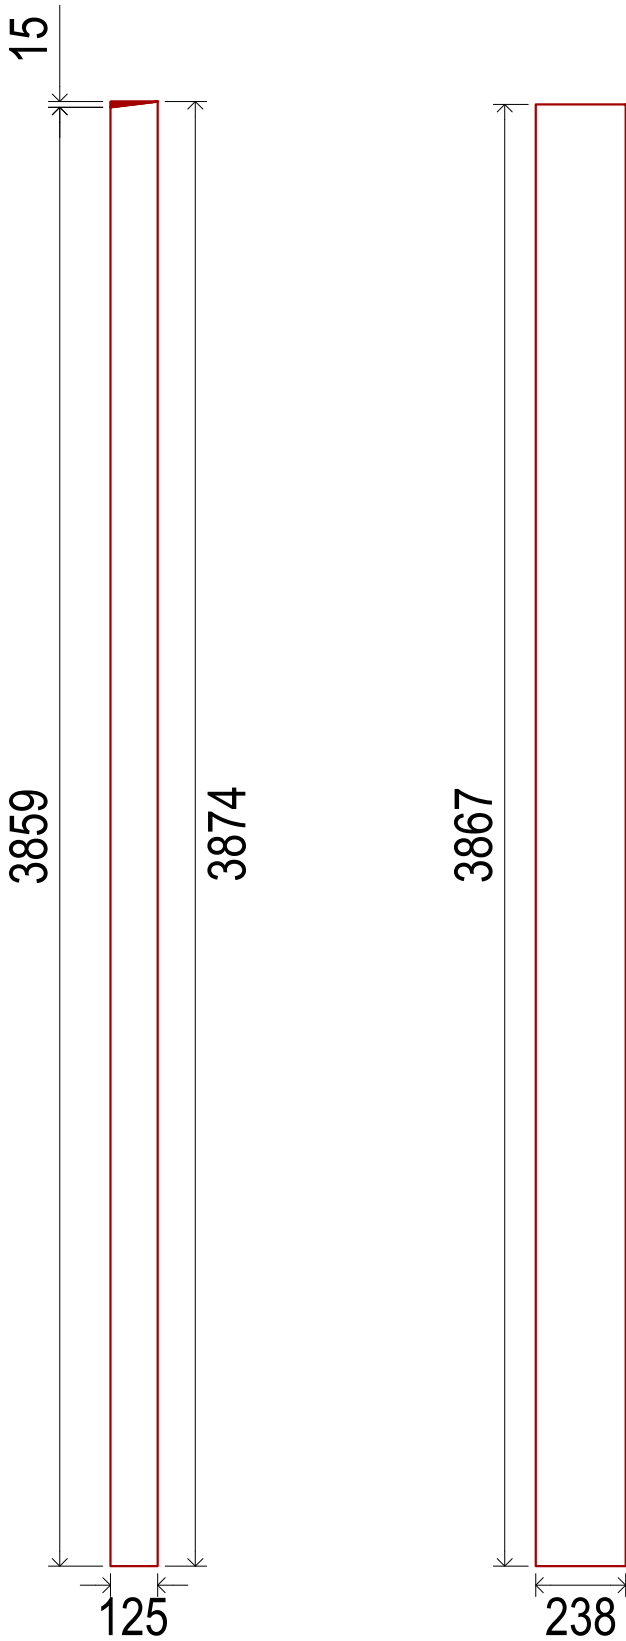


CUTTING WEB OF SC102

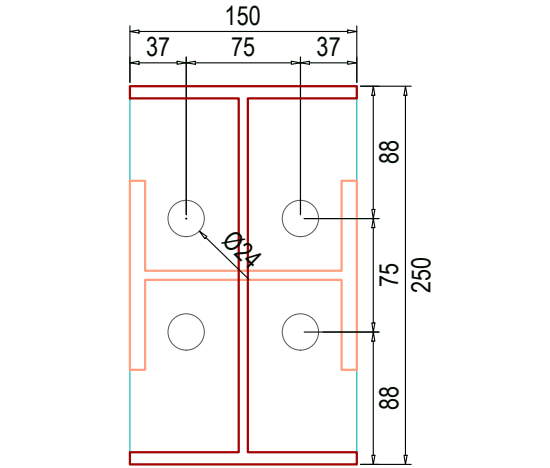

DETAILS OF CP250x150x16
(16 mm Thickness)
Qty: 08Nos

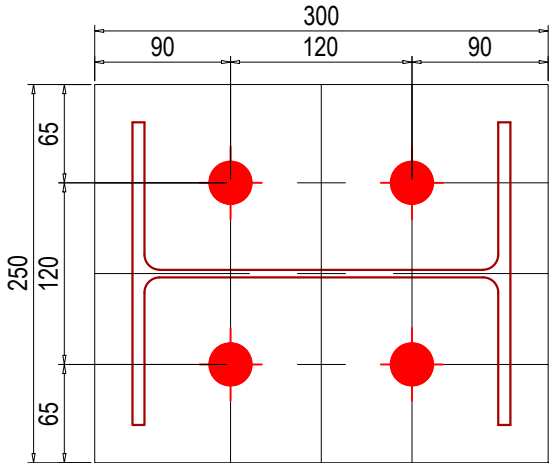

DETAILS OF BP01
(THICK: 20mm);Total: 16Nos.

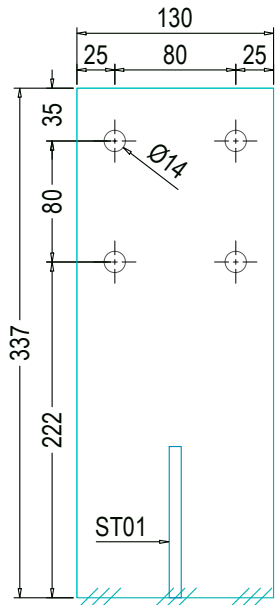

DETAILS OF PC337*8
(THICKNESS 8mm)
Qty: 04Nos

M/S. B.S. ENGINEERING
Factory: Plot-09, N,S Road,
Block-H, Sector-2,
Jahirul Islam City,
Aftabnagar, Dhaka-1212.

PROJECT:
PROPOSED SINGLE-STORIED
PRE-FABRICATED STEEL
BUILDING.

CLIENT:
MR. JAHANGIR

REFERENCE NO.:
BS-26-031

DESIGNER:

MD. REJAUL KARIM
B.Sc. ENGINEER (CIVIL), MIEB






MD. RIFAT MAHMUD SAJIB
B.Sc. ENGINEER (CIVIL), MIEB

DRAWN BY:
Polash

DRAWING TITLE:
DETAIL SC102

DATE:
23.07.2026

REV.:	SCALE:	DWG.NO.
00	NTS	ST-12

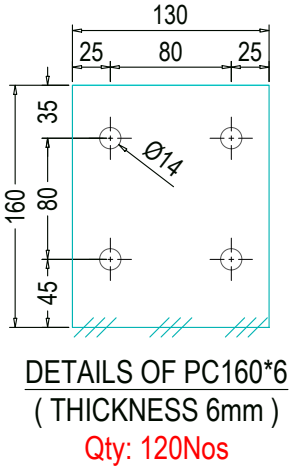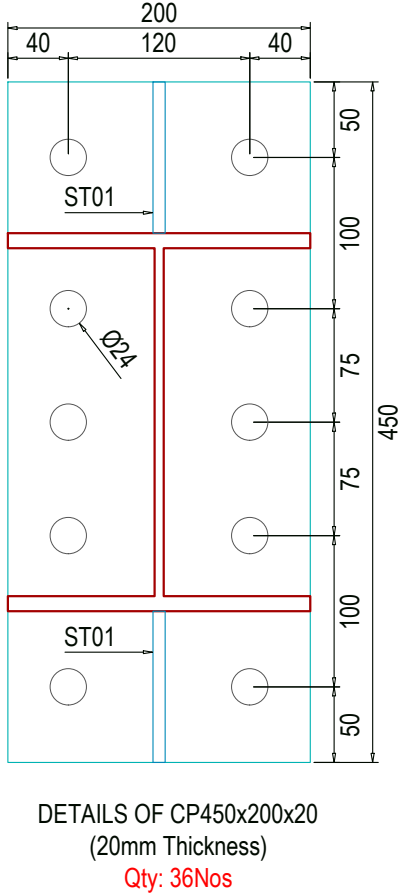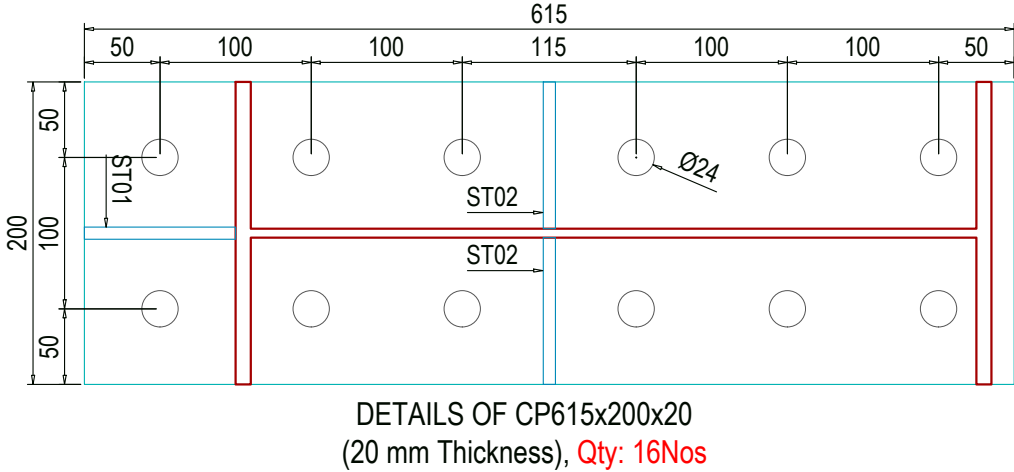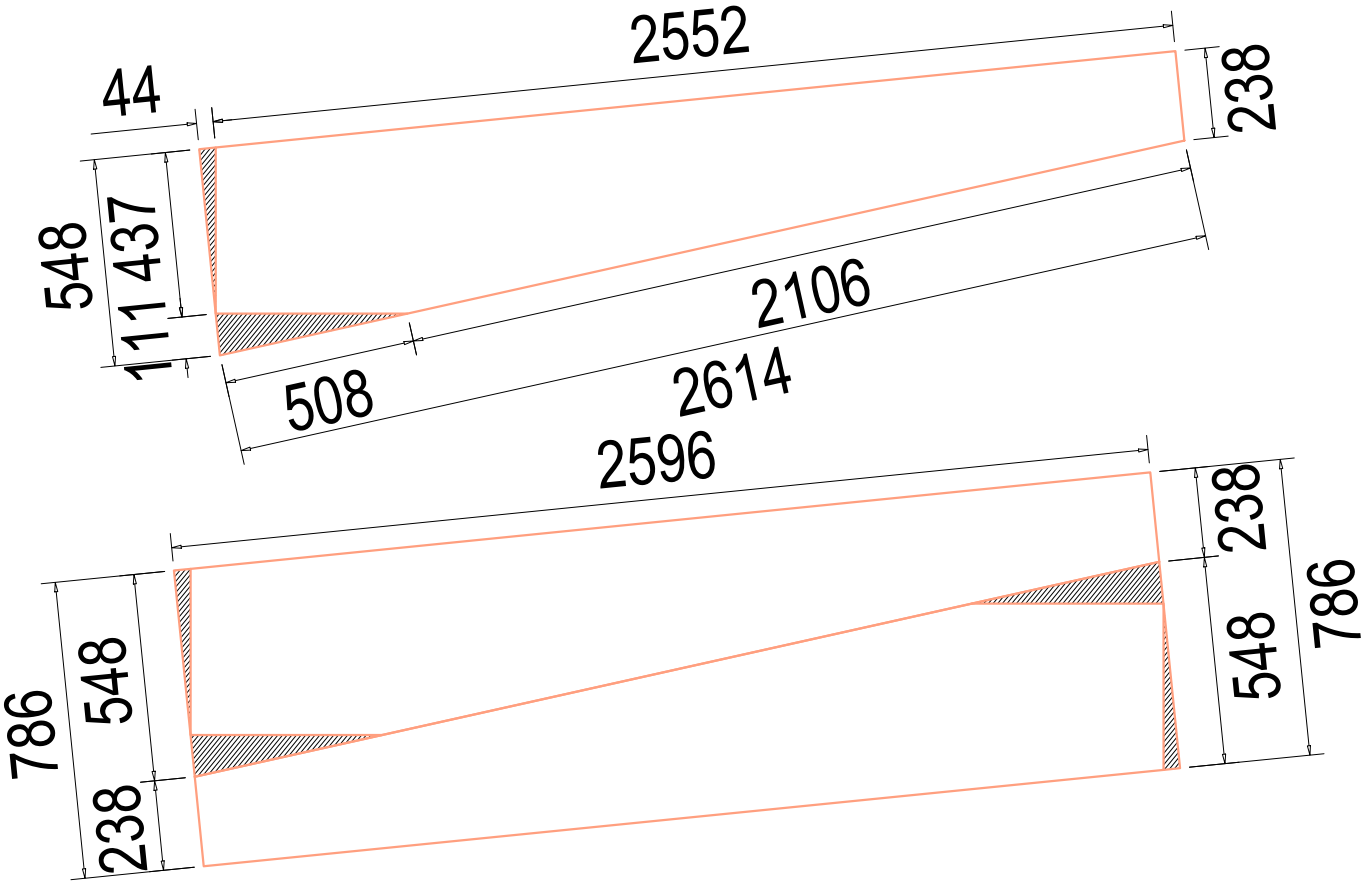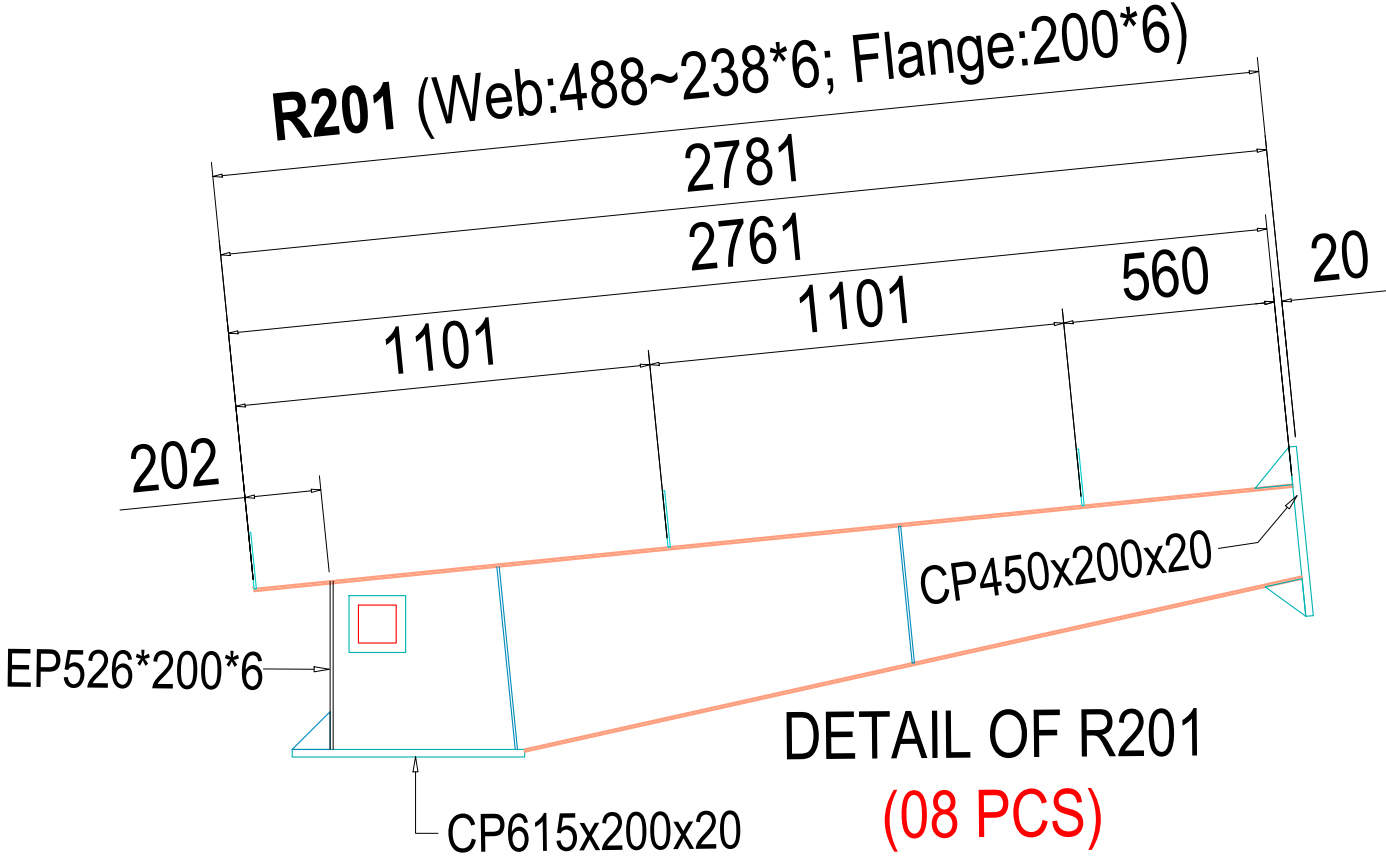

M/S. B.S. ENGINEERING
Factory: Plot-09, N,S Road,
Block-H, Sector-2,
Jahirul Islam City,
Aftabnagar, Dhaka-1212.

PROJECT:
PROPOSED SINGLE-STORIED
PRE-FABRICATED STEEL
BUILDING.

CLIENT:
MR. JAHANGIR

REFERENCE NO.:
BS-26-031

DESIGNER:

MD. REJAUL KARIM
B.Sc. ENGINEER (CIVIL), MIEB


MD. RIFAT MAHMUD SAJIB
B.Sc. ENGINEER (CIVIL), MIEB

DRAWN BY:
Polash


DRAWING TITLE:
DETAIL R201

DATE:
23.07.2026



REV.:	SCALE:	DWG.NO.
00	NTS	ST-13

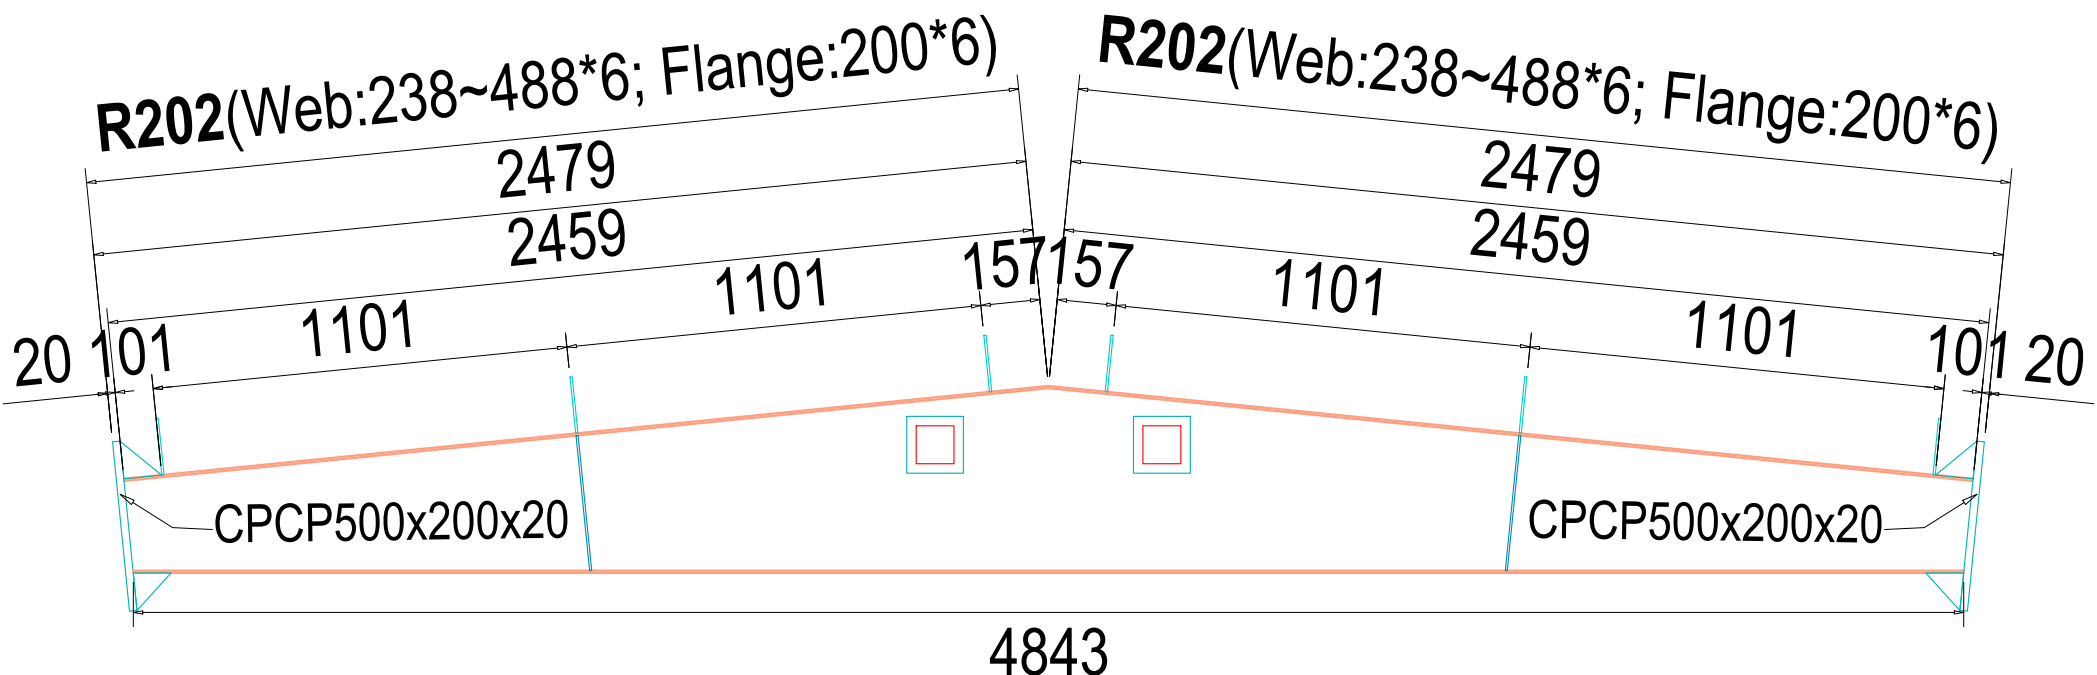


DETAIL OF R203
(04 PCS)

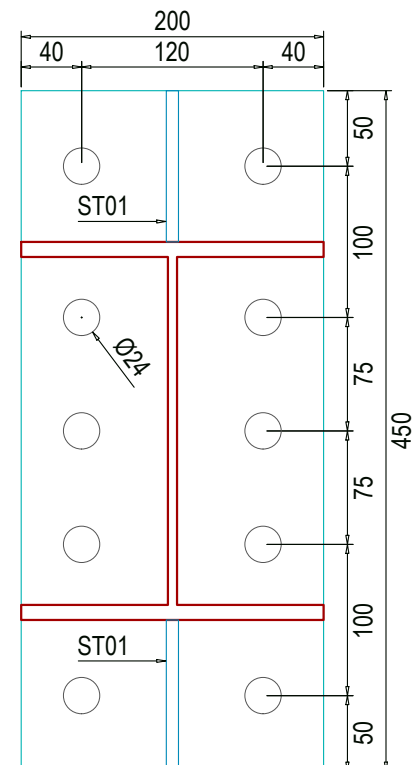

DETAILS OF CP450x200x20
(20mm Thickness)
Qty: 36Nos

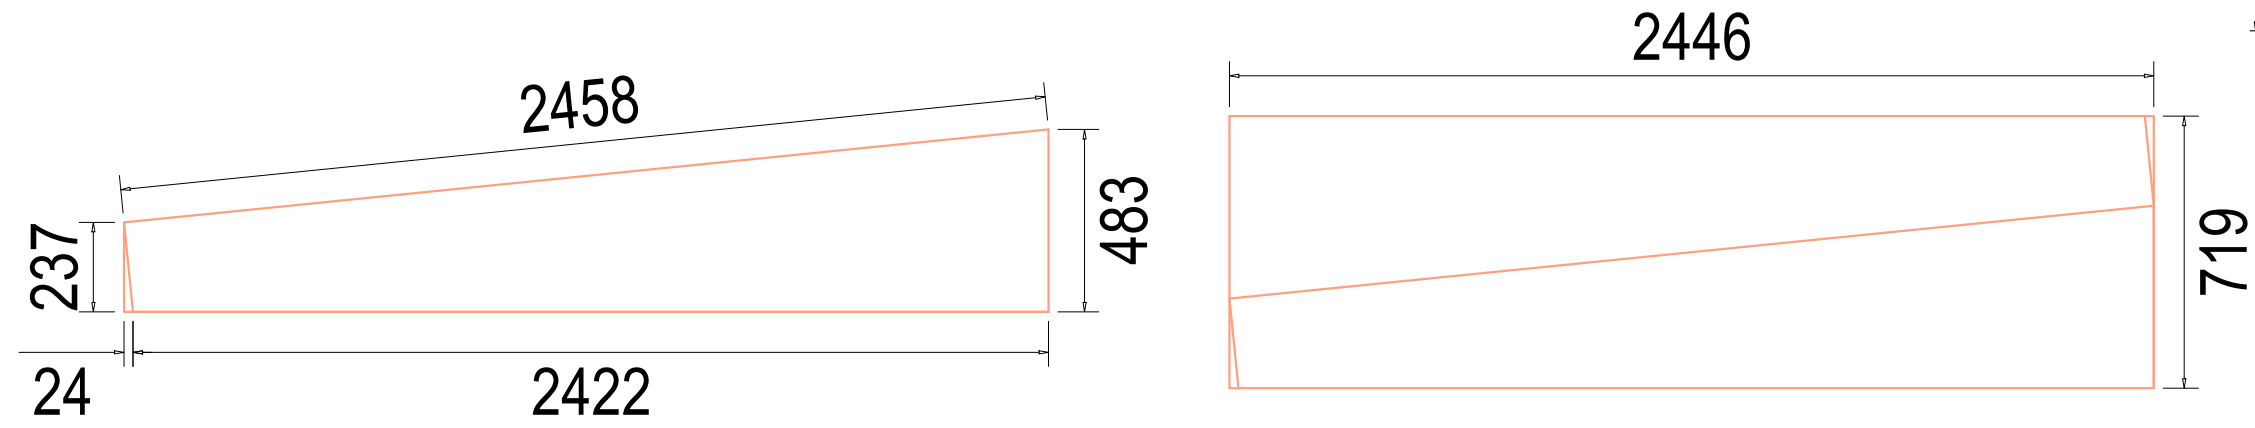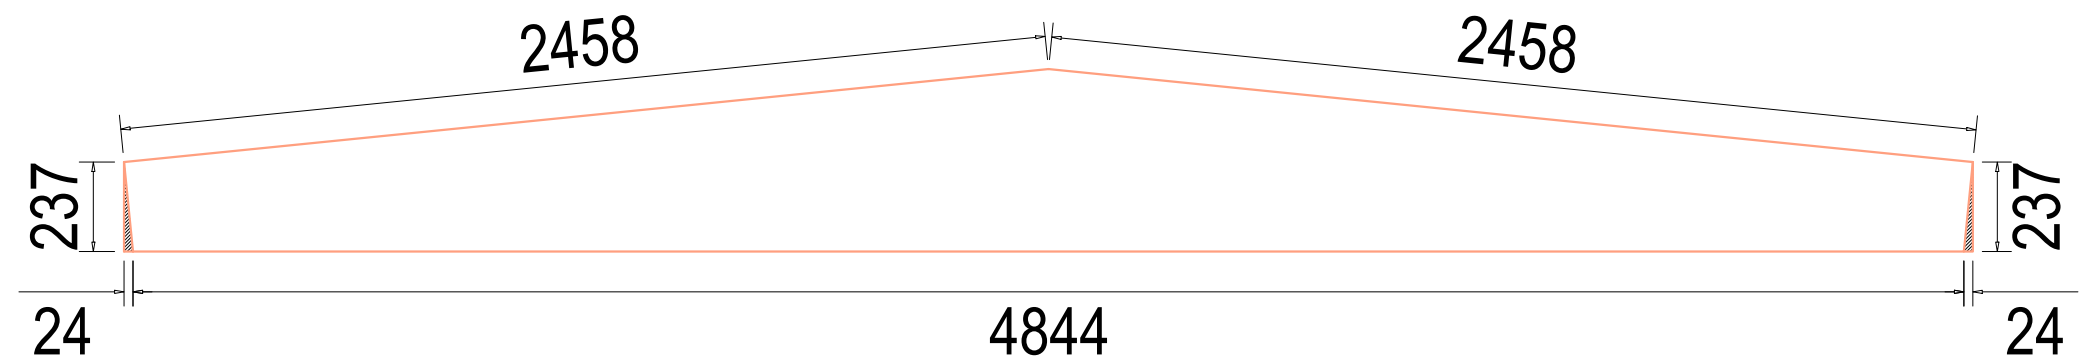

CUTTING WEB OF R203

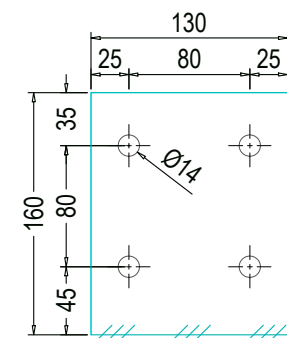

DETAILS OF PC160*6
(THICKNESS 6mm)
Qty: 120Nos

M/S. B.S. ENGINEERING
Factory: Plot-09, N,S Road,
Block-H, Sector-2,
Jahirul Islam City,
Aftabnagar, Dhaka-1212.

PROJECT:
PROPOSED SINGLE-STORIED
PRE-FABRICATED STEEL
BUILDING.

CLIENT:
MR. JAHANGIR

REFERENCE NO.:
BS-26-031

DESIGNER:

MD. REJAUL KARIM
B.Sc. ENGINEER (CIVIL), MIEB



MD. RIFAT MAHMUD SAJIB
B.Sc. ENGINEER (CIVIL), MIEB

DRAWN BY:
Polash

DRAWING TITLE:
DETAIL R203

DATE:
23.07.2026

REV.:	SCALE:	DWG.NO.
00	NTS	ST-14

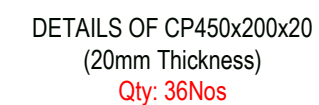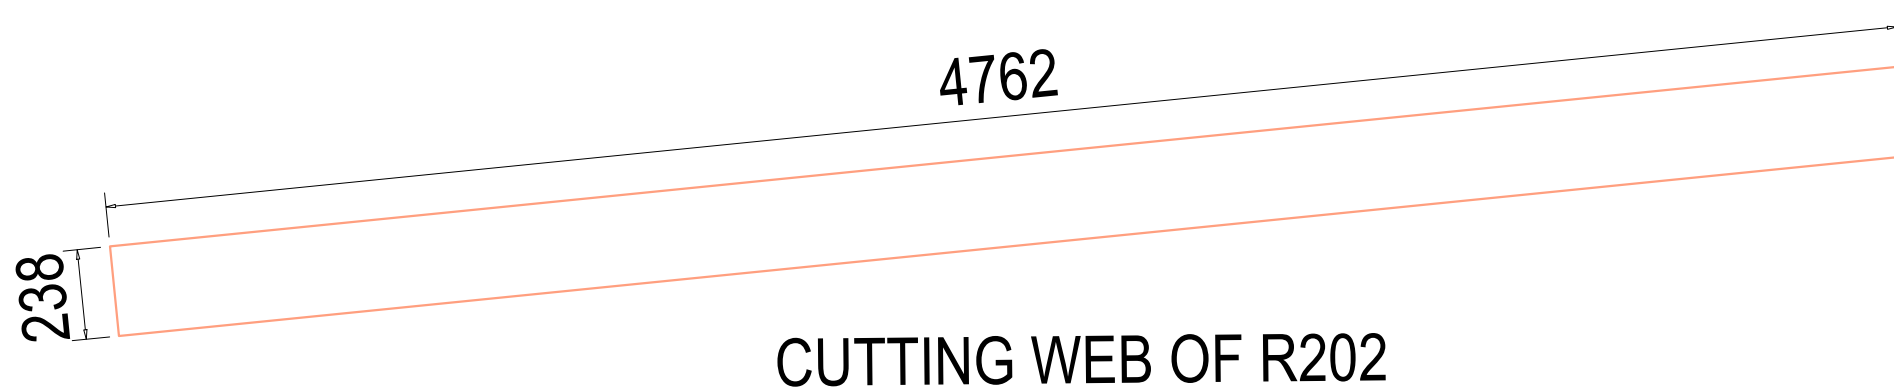

Factory: Plot-09, N,S Road,
Block-H, Sector-2,
Jahirul Islam City,
Aftabnagar, Dhaka-1212.

PROPOSED SINGLE-STORIED
PRE-FABRICATED STEEL
BUILDING.

MR. JAHANGIR

BS-26-031

MD. REJAUL KARIM
B.Sc. ENGINEER (CIVIL), MIEB




MD. RIFAT MAHMUD SAJIB
B.Sc. ENGINEER (CIVIL), MIEB

Polash


DETAIL R202

23.07.2026


REV.:	SCALE:	DWG.NO.
00	NTS	ST-15

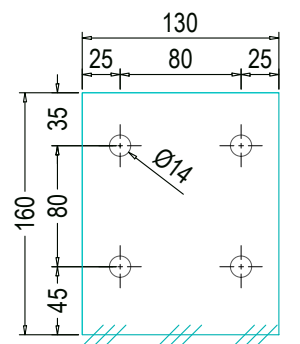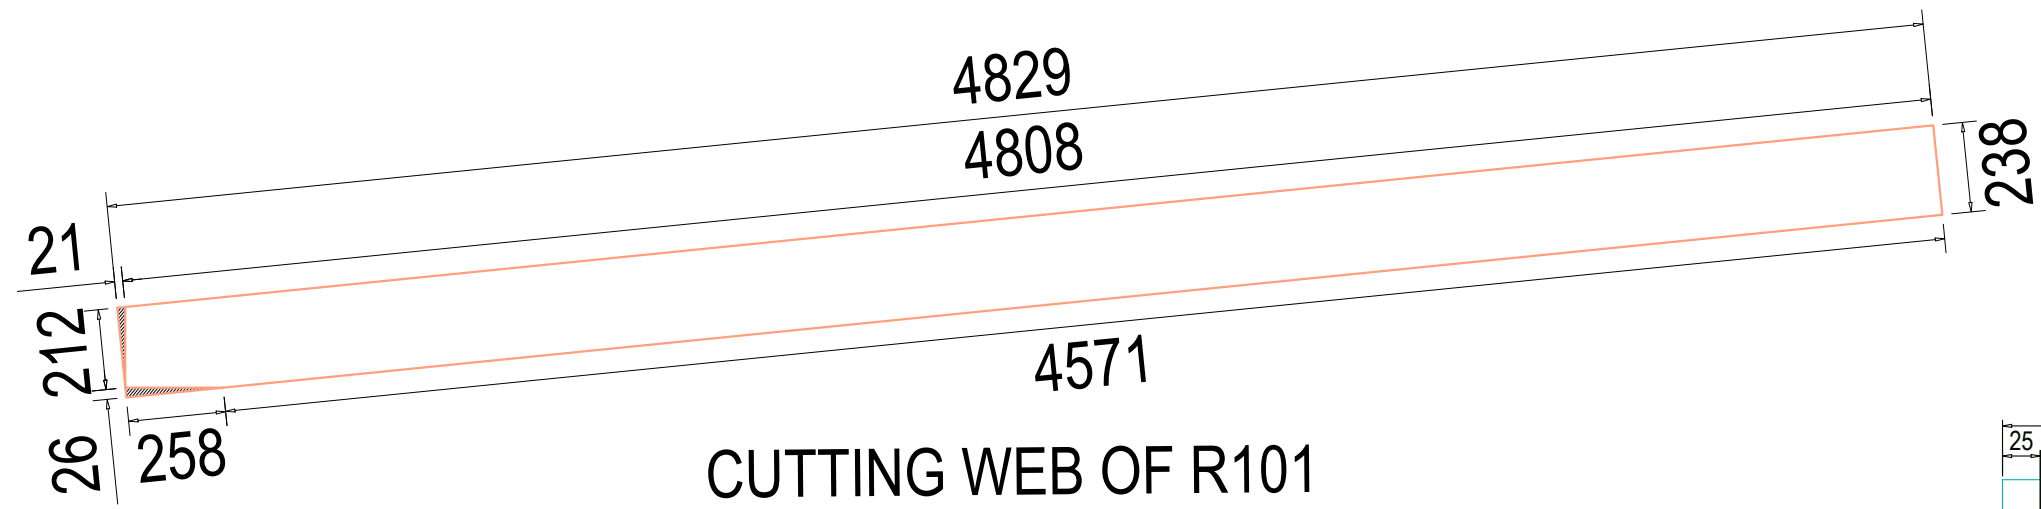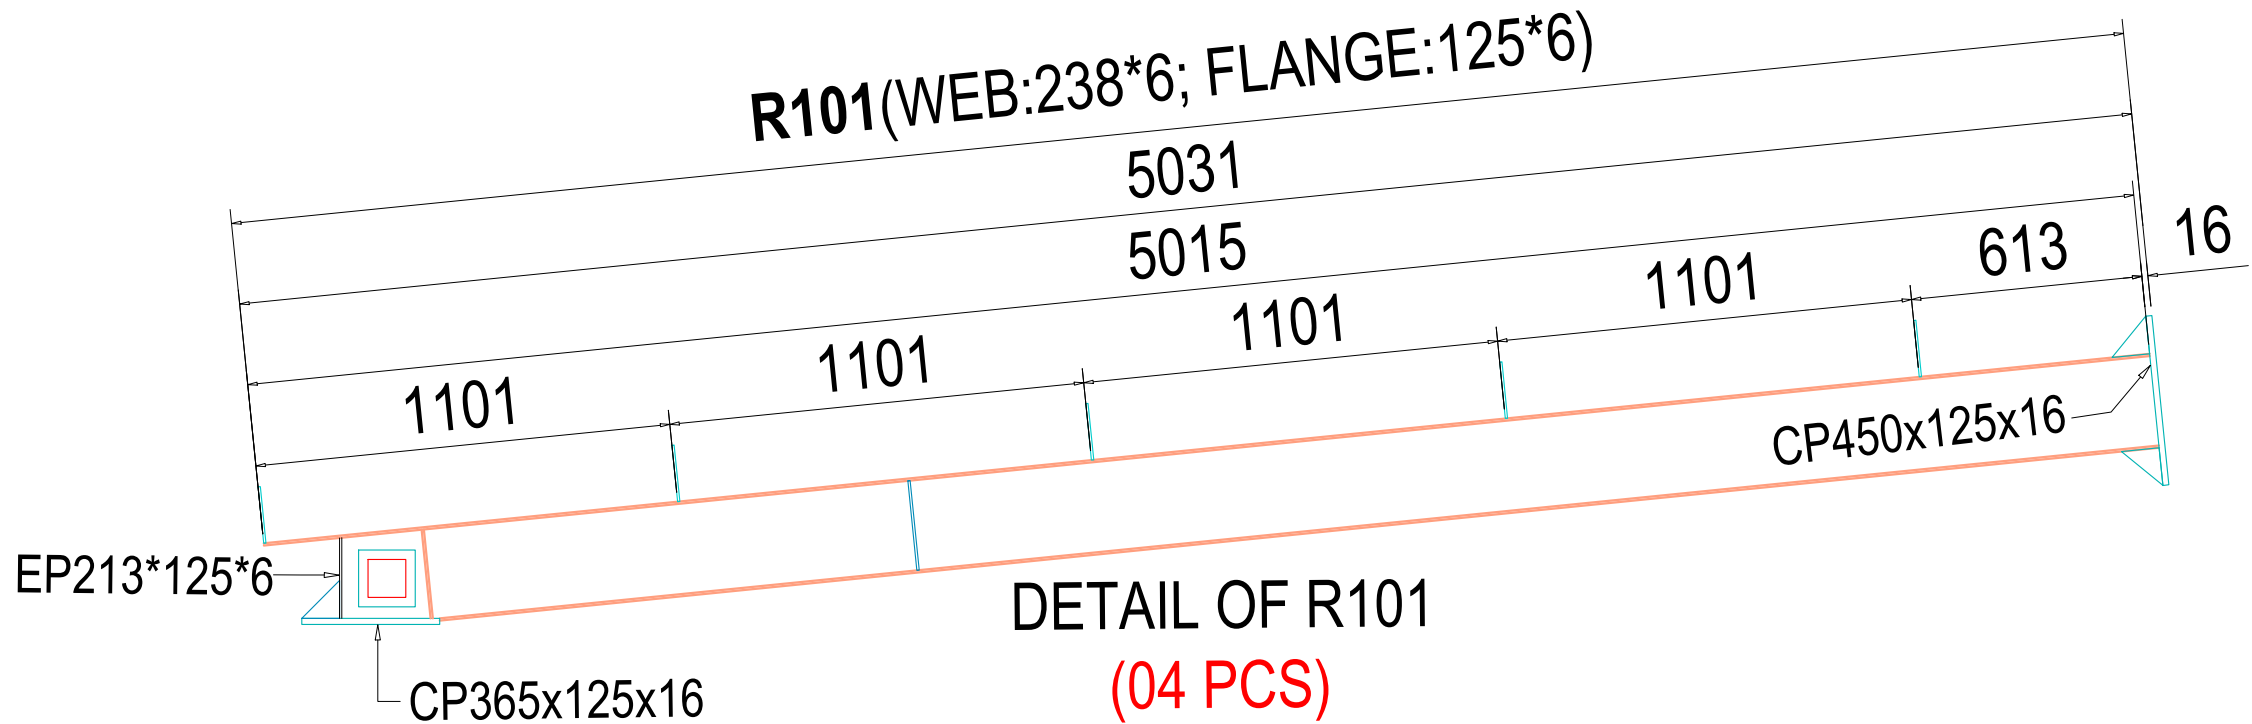

DETAILS OF PC160*6
(THICKNESS 6mm)
Qty: 120Nos

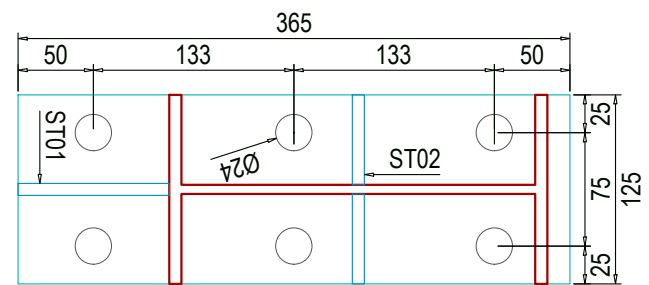

DETAILS OF CP365x125x16
(16mm Thickness)
Qty: 08Nos

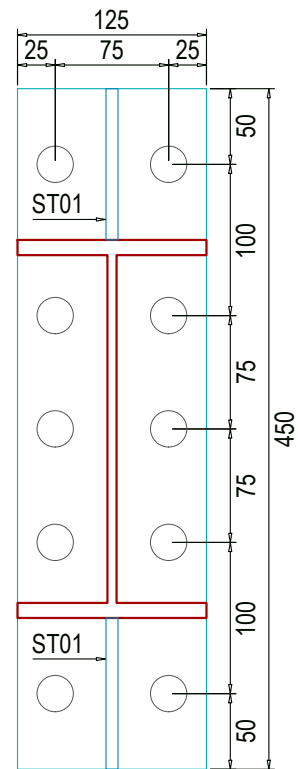

DETAILS OF CP450x125x16
(16mm Thickness)
Qty: 08Nos

M/S. B.S. ENGINEERING
Factory: Plot-09, N,S Road,
Block-H, Sector-2,
Jahirul Islam City,
Aftabnagar, Dhaka-1212.

PROJECT:
PROPOSED SINGLE-STORIED
PRE-FABRICATED STEEL
BUILDING.

CLIENT:
MR. JAHANGIR

REFERENCE NO.:
BS-26-031

DESIGNER:

MD. REJAUL KARIM
B.Sc. ENGINEER (CIVIL), MIEB


MD. RIFAT MAHMUD SAJIB
B.Sc. ENGINEER (CIVIL), MIEB

DRAWN BY:
Polash

DRAWING TITLE:
DETAIL R101


DATE:
23.07.2026

REV.:	SCALE:	DWG.NO.
00	NTS	ST-16

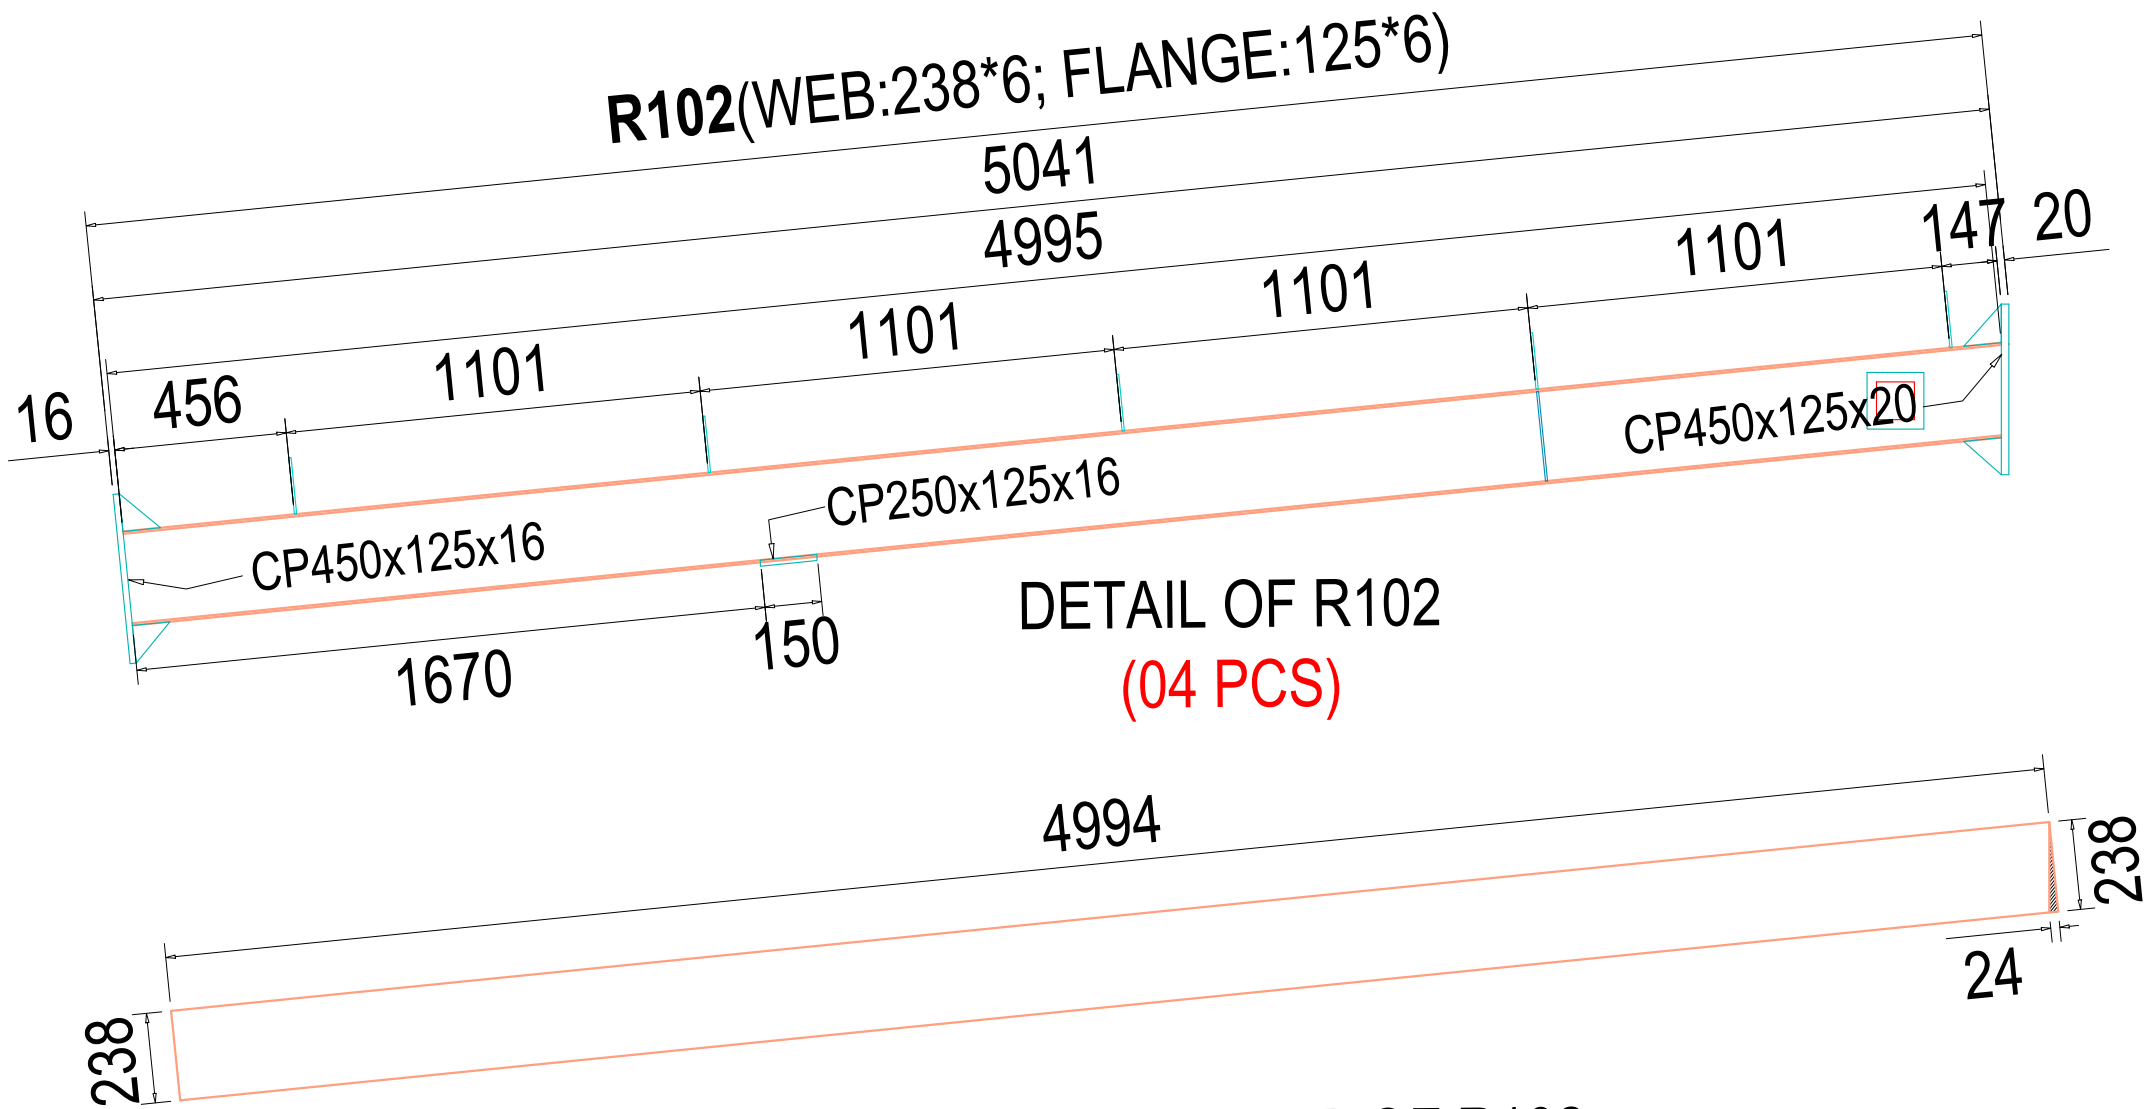


DETAIL OF R102
(04 PCS)


CUTTING WEB OF R102

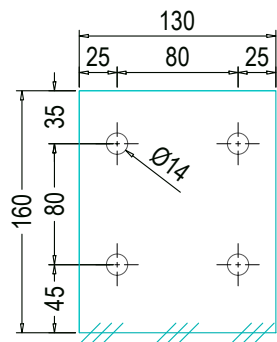

DETAILS OF PC160*6
(THICKNESS 6mm)
Qty: 120Nos

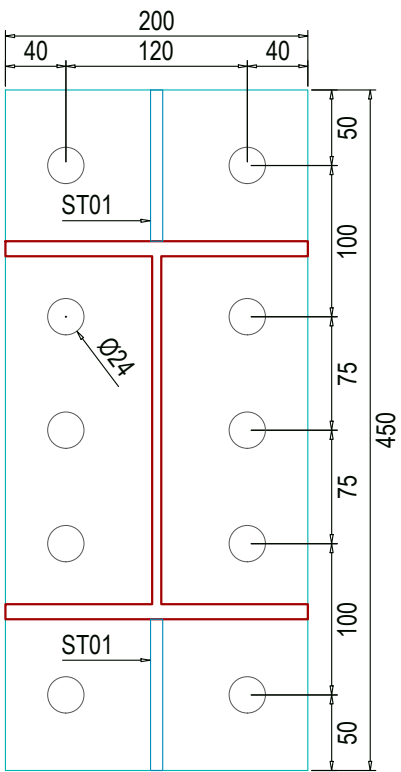

DETAILS OF CP450x200x20
(20mm Thickness)
Qty: 36Nos

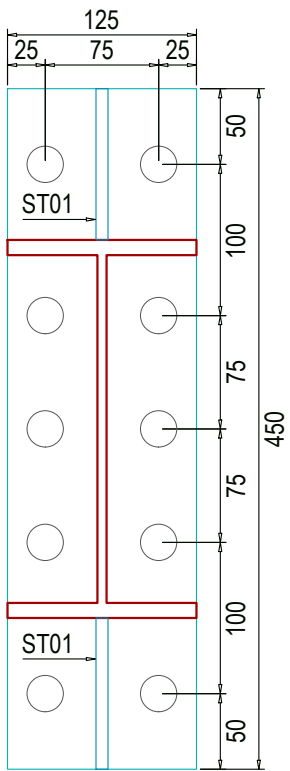

DETAILS OF CP450x125x16
(16mm Thickness)
Qty: 08Nos

M/S. B.S. ENGINEERING
Factory: Plot-09, N,S Road,
Block-H, Sector-2,
Jahirul Islam City,
Aftabnagar, Dhaka-1212.

PROJECT:
PROPOSED SINGLE-STORIED
PRE-FABRICATED STEEL
BUILDING.

CLIENT:
MR. JAHANGIR

REFERENCE NO.:
BS-26-031

DESIGNER:

MD. REJAUL KARIM
B.Sc. ENGINEER (CIVIL), MIEB


MD. RIFAT MAHMUD SAJIB
B.Sc. ENGINEER (CIVIL), MIEB

DRAWN BY:
Polash

DRAWING TITLE:
DETAIL R102



DATE:
23.07.2026

REV.:	SCALE:	DWG.NO.
00	NTS	ST-17

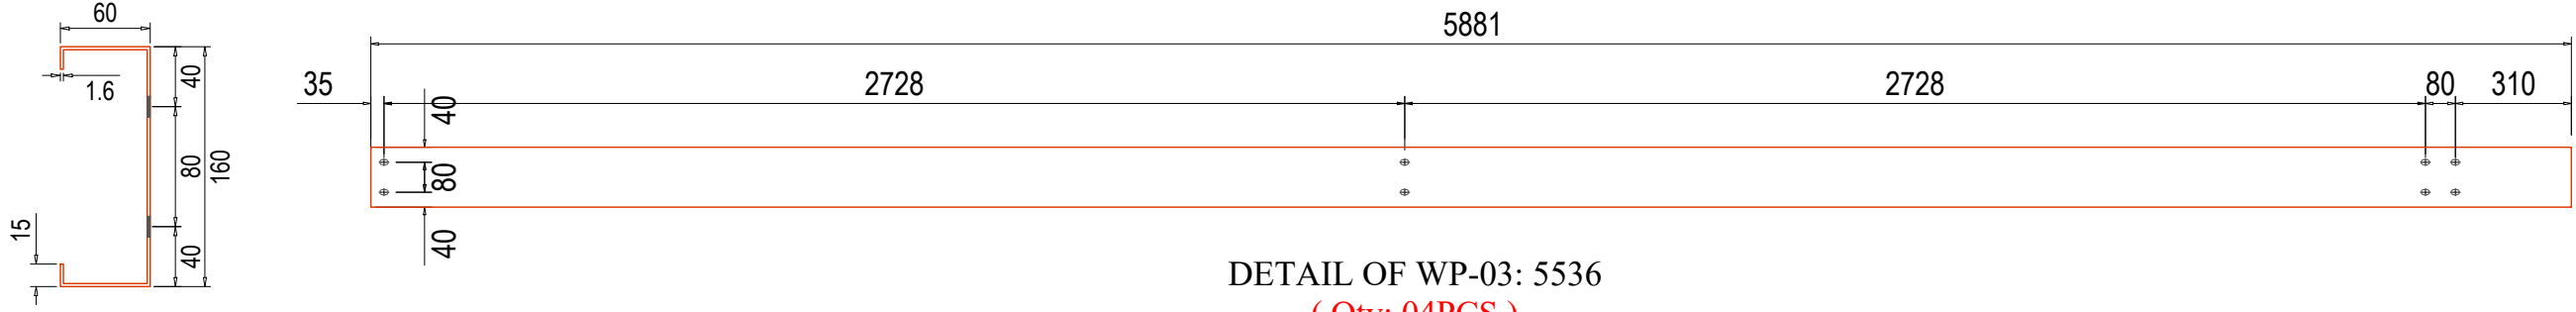


DETAIL OF WP-03: 5536
(Qty: 04PCS)

ST-18

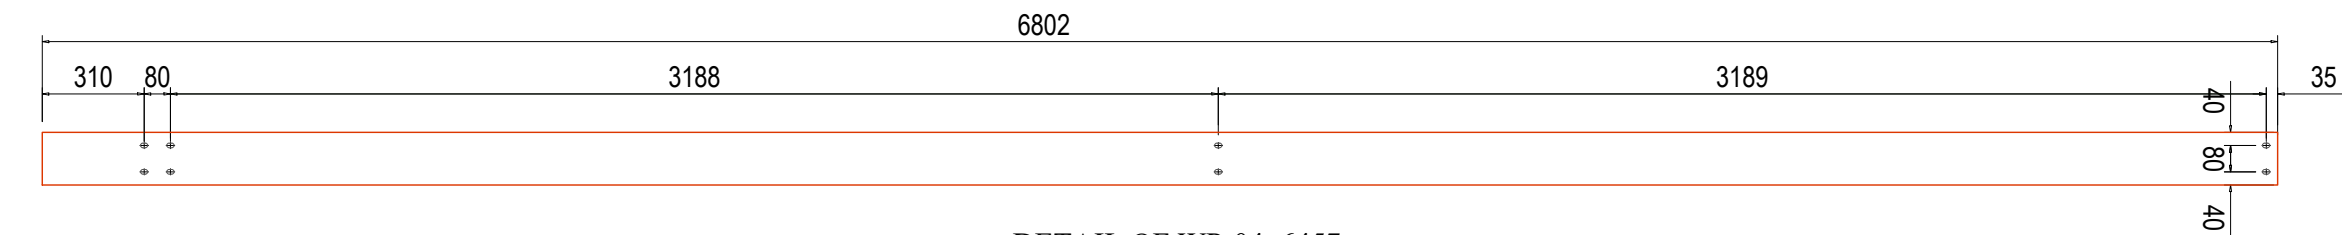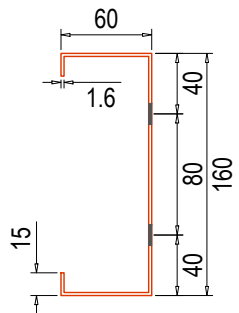

DETAIL OF WP-04: 6457
(Qty: 04PCS)

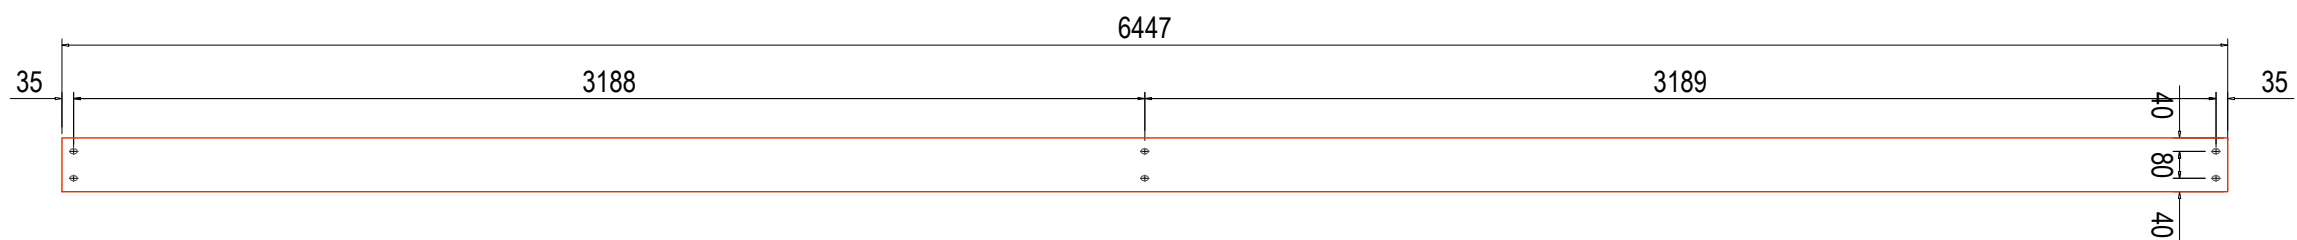

DETAIL OF WP-05: 6457
(Qty: 02PCS)

Factory: Plot-09, N,S Road,
Block-H, Sector-2,
Jahirul Islam City,
Aftabnagar, Dhaka-1212.

PROJECT:

PROPOSED SINGLE-STORIED
PRE-FABRICATED STEEL
BUILDING.

CLIENT:

MR. JAHANGIR

REFERENCE NO.:

BS-26-031

DESIGNER:

MD. REJAUL KARIM
B.Sc. ENGINEER (CIVIL), MIEB

MD. RIFAT MAHMUD SAJIB
B.Sc. ENGINEER (CIVIL), MIEB

DRAWN BY:

Polash

DRAWING TITLE:

DETAIL OF PURLIN

DATE:

12.08.2026

REV.:	SCALE:	DWG.NO.
00	NTS	ST-19