


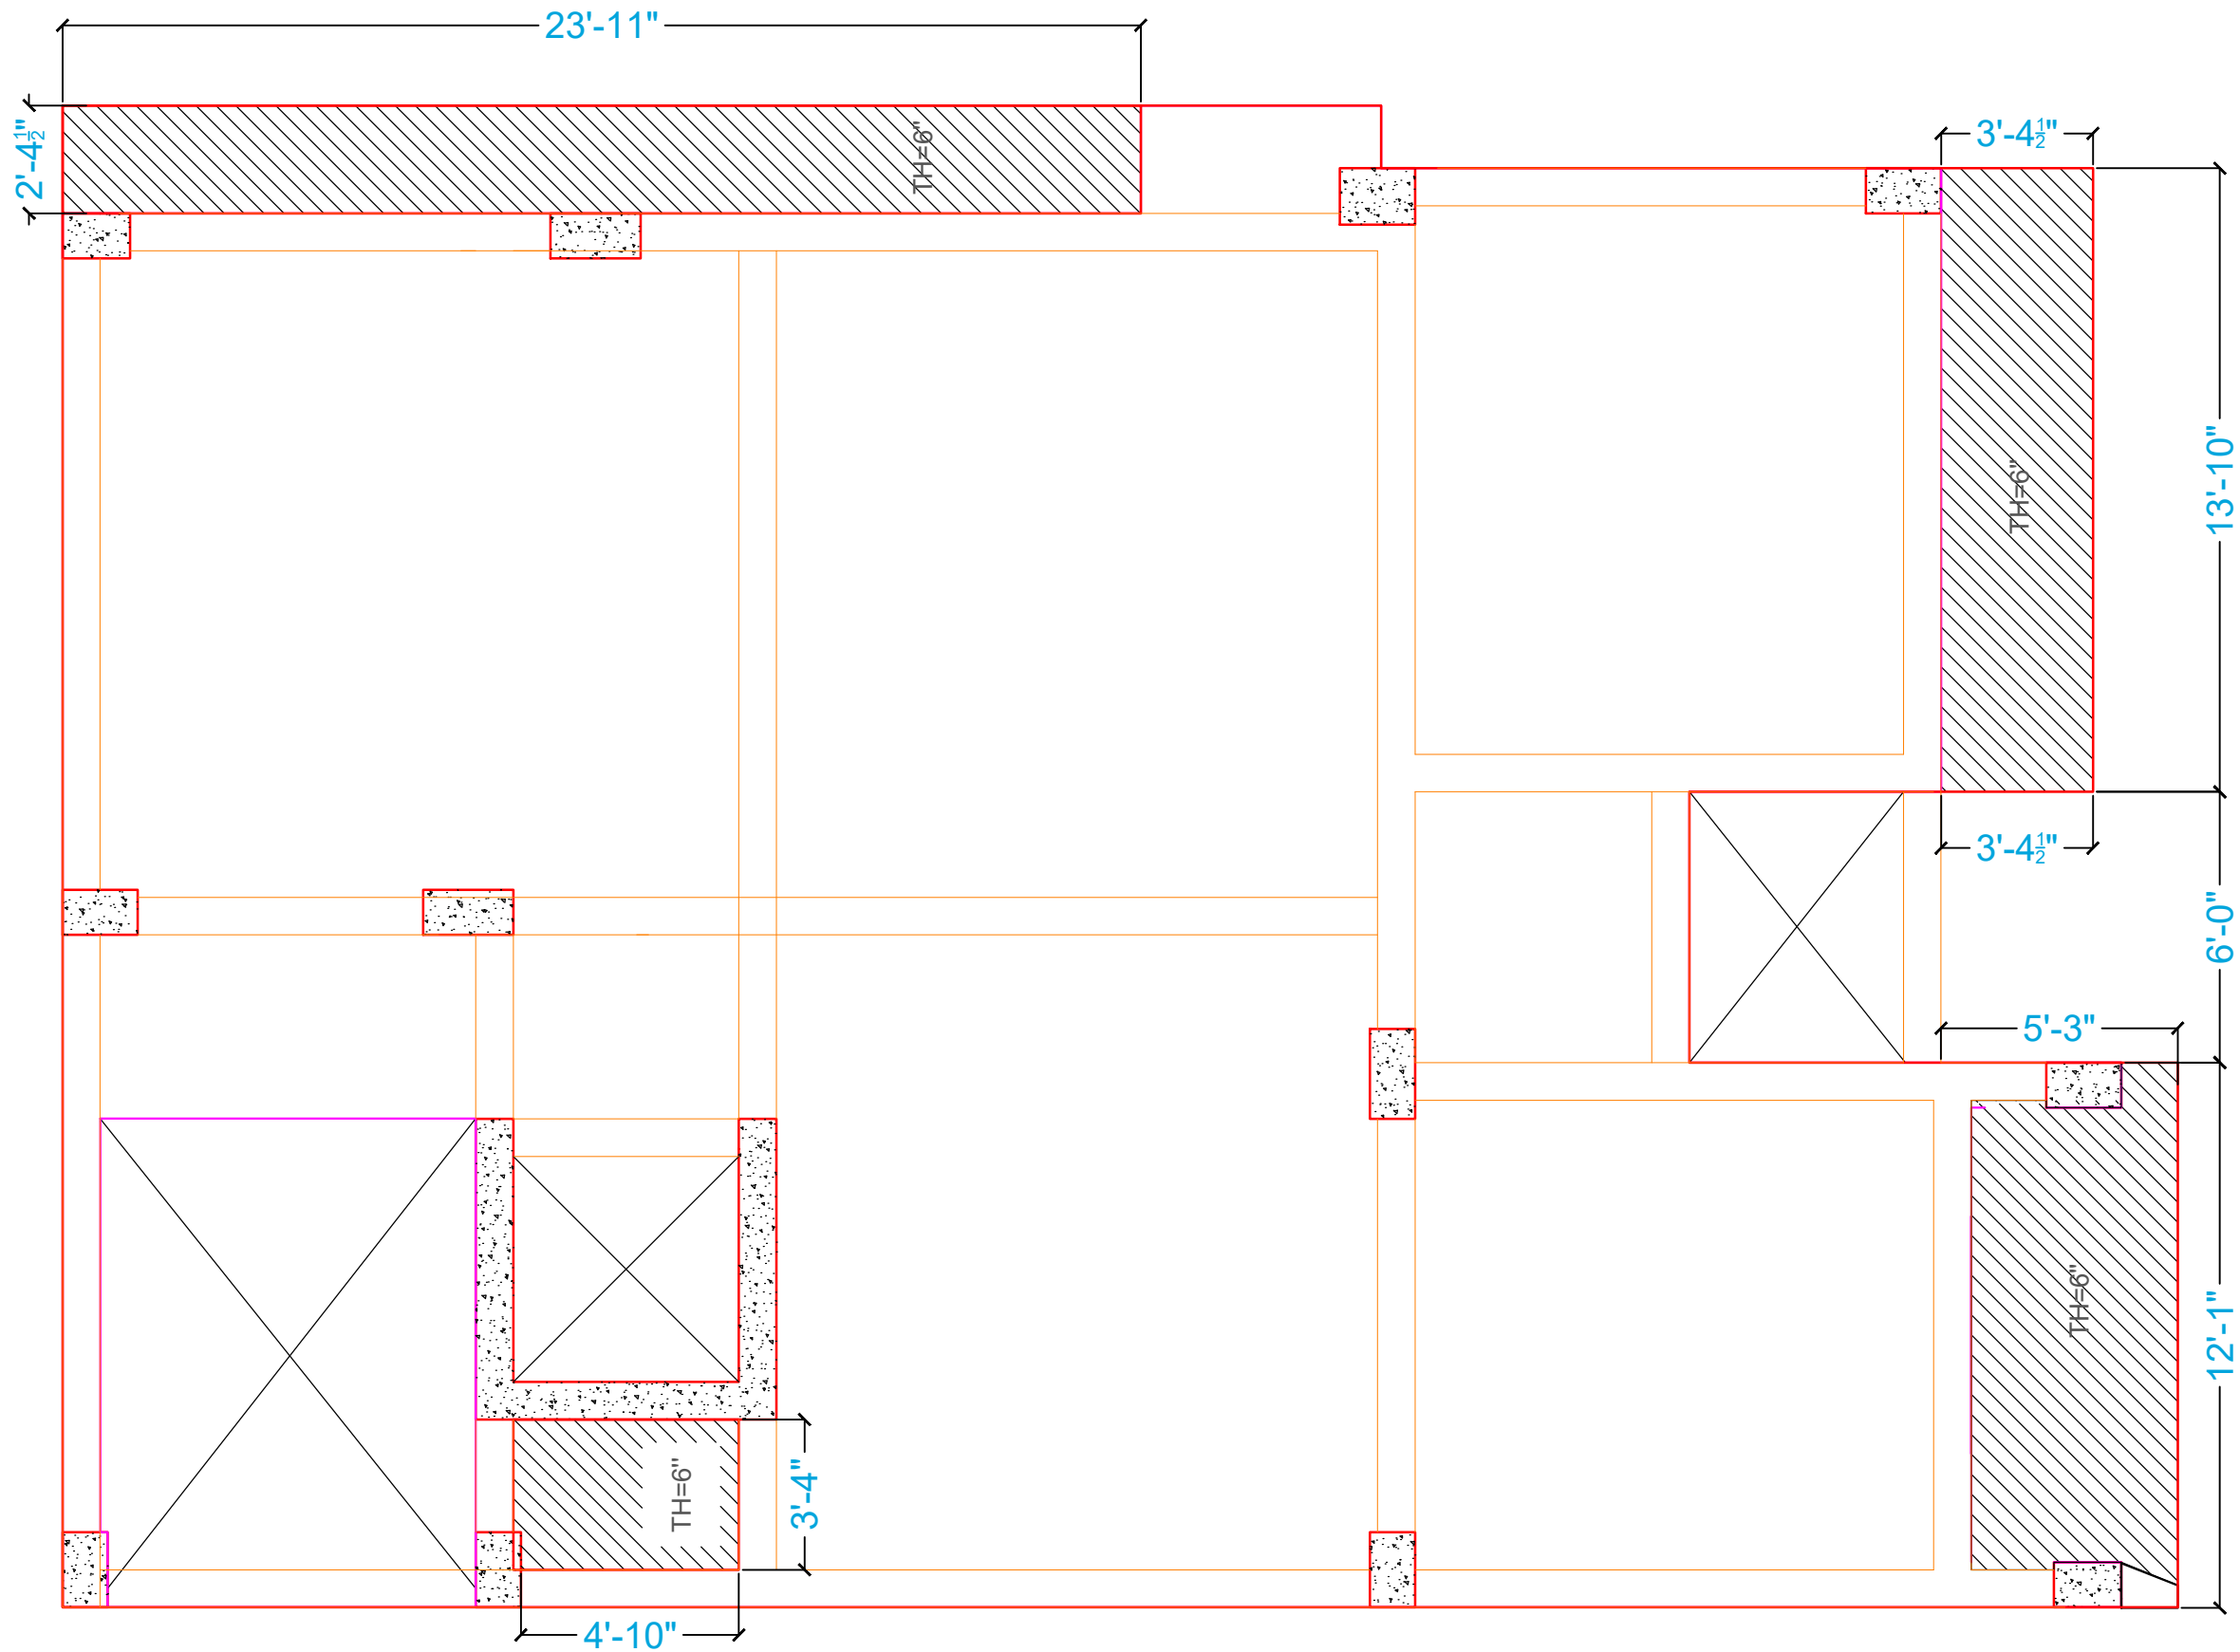

PROJECT

PROPOSED G+6= 07 (SEVEN) STORIED RESIDENTIAL
BUILDING PLAN (TYPE A-A3) ON PLOT-9287,
ROAD-12, BLOCK-N, BASUNDHARA RESIDENTIAL
AREA, DHAKA.

CONSULTANT



**EDIFICE CONSTRUCTION &
CONSULTANTS**
H-62/5/E , Rupayan,
P&F Square,Flat-6A & 6B
North Sagufta,New Road
Kalshi,Dhaka-1216
E-mail:nuralam.edifice@gmail.com
cell-01796585611,01685663316

OWNER/CLIENT

MAHAMUDAL HASSAN

ARCHITECT

AR. RAFIUL ISLAM RAFI
B.ARCH(SUST)

CHECKED & APPROVED BY

ENGR. MD. NUR ALAM
B.Sc. in CIVIL ENGG.
FIEB-11295

DRAWN BY

MD. MOHAIMENUL ISLAM

DRAWING TITLE

STUCTURAL
WORKING DRAWING

SHEET TITLE


3 RD FLOOR ROOF
BEAM BOTTOM SALB

SUBMISSION DATE:-

05.02.2026

SHEET NO:

A-01

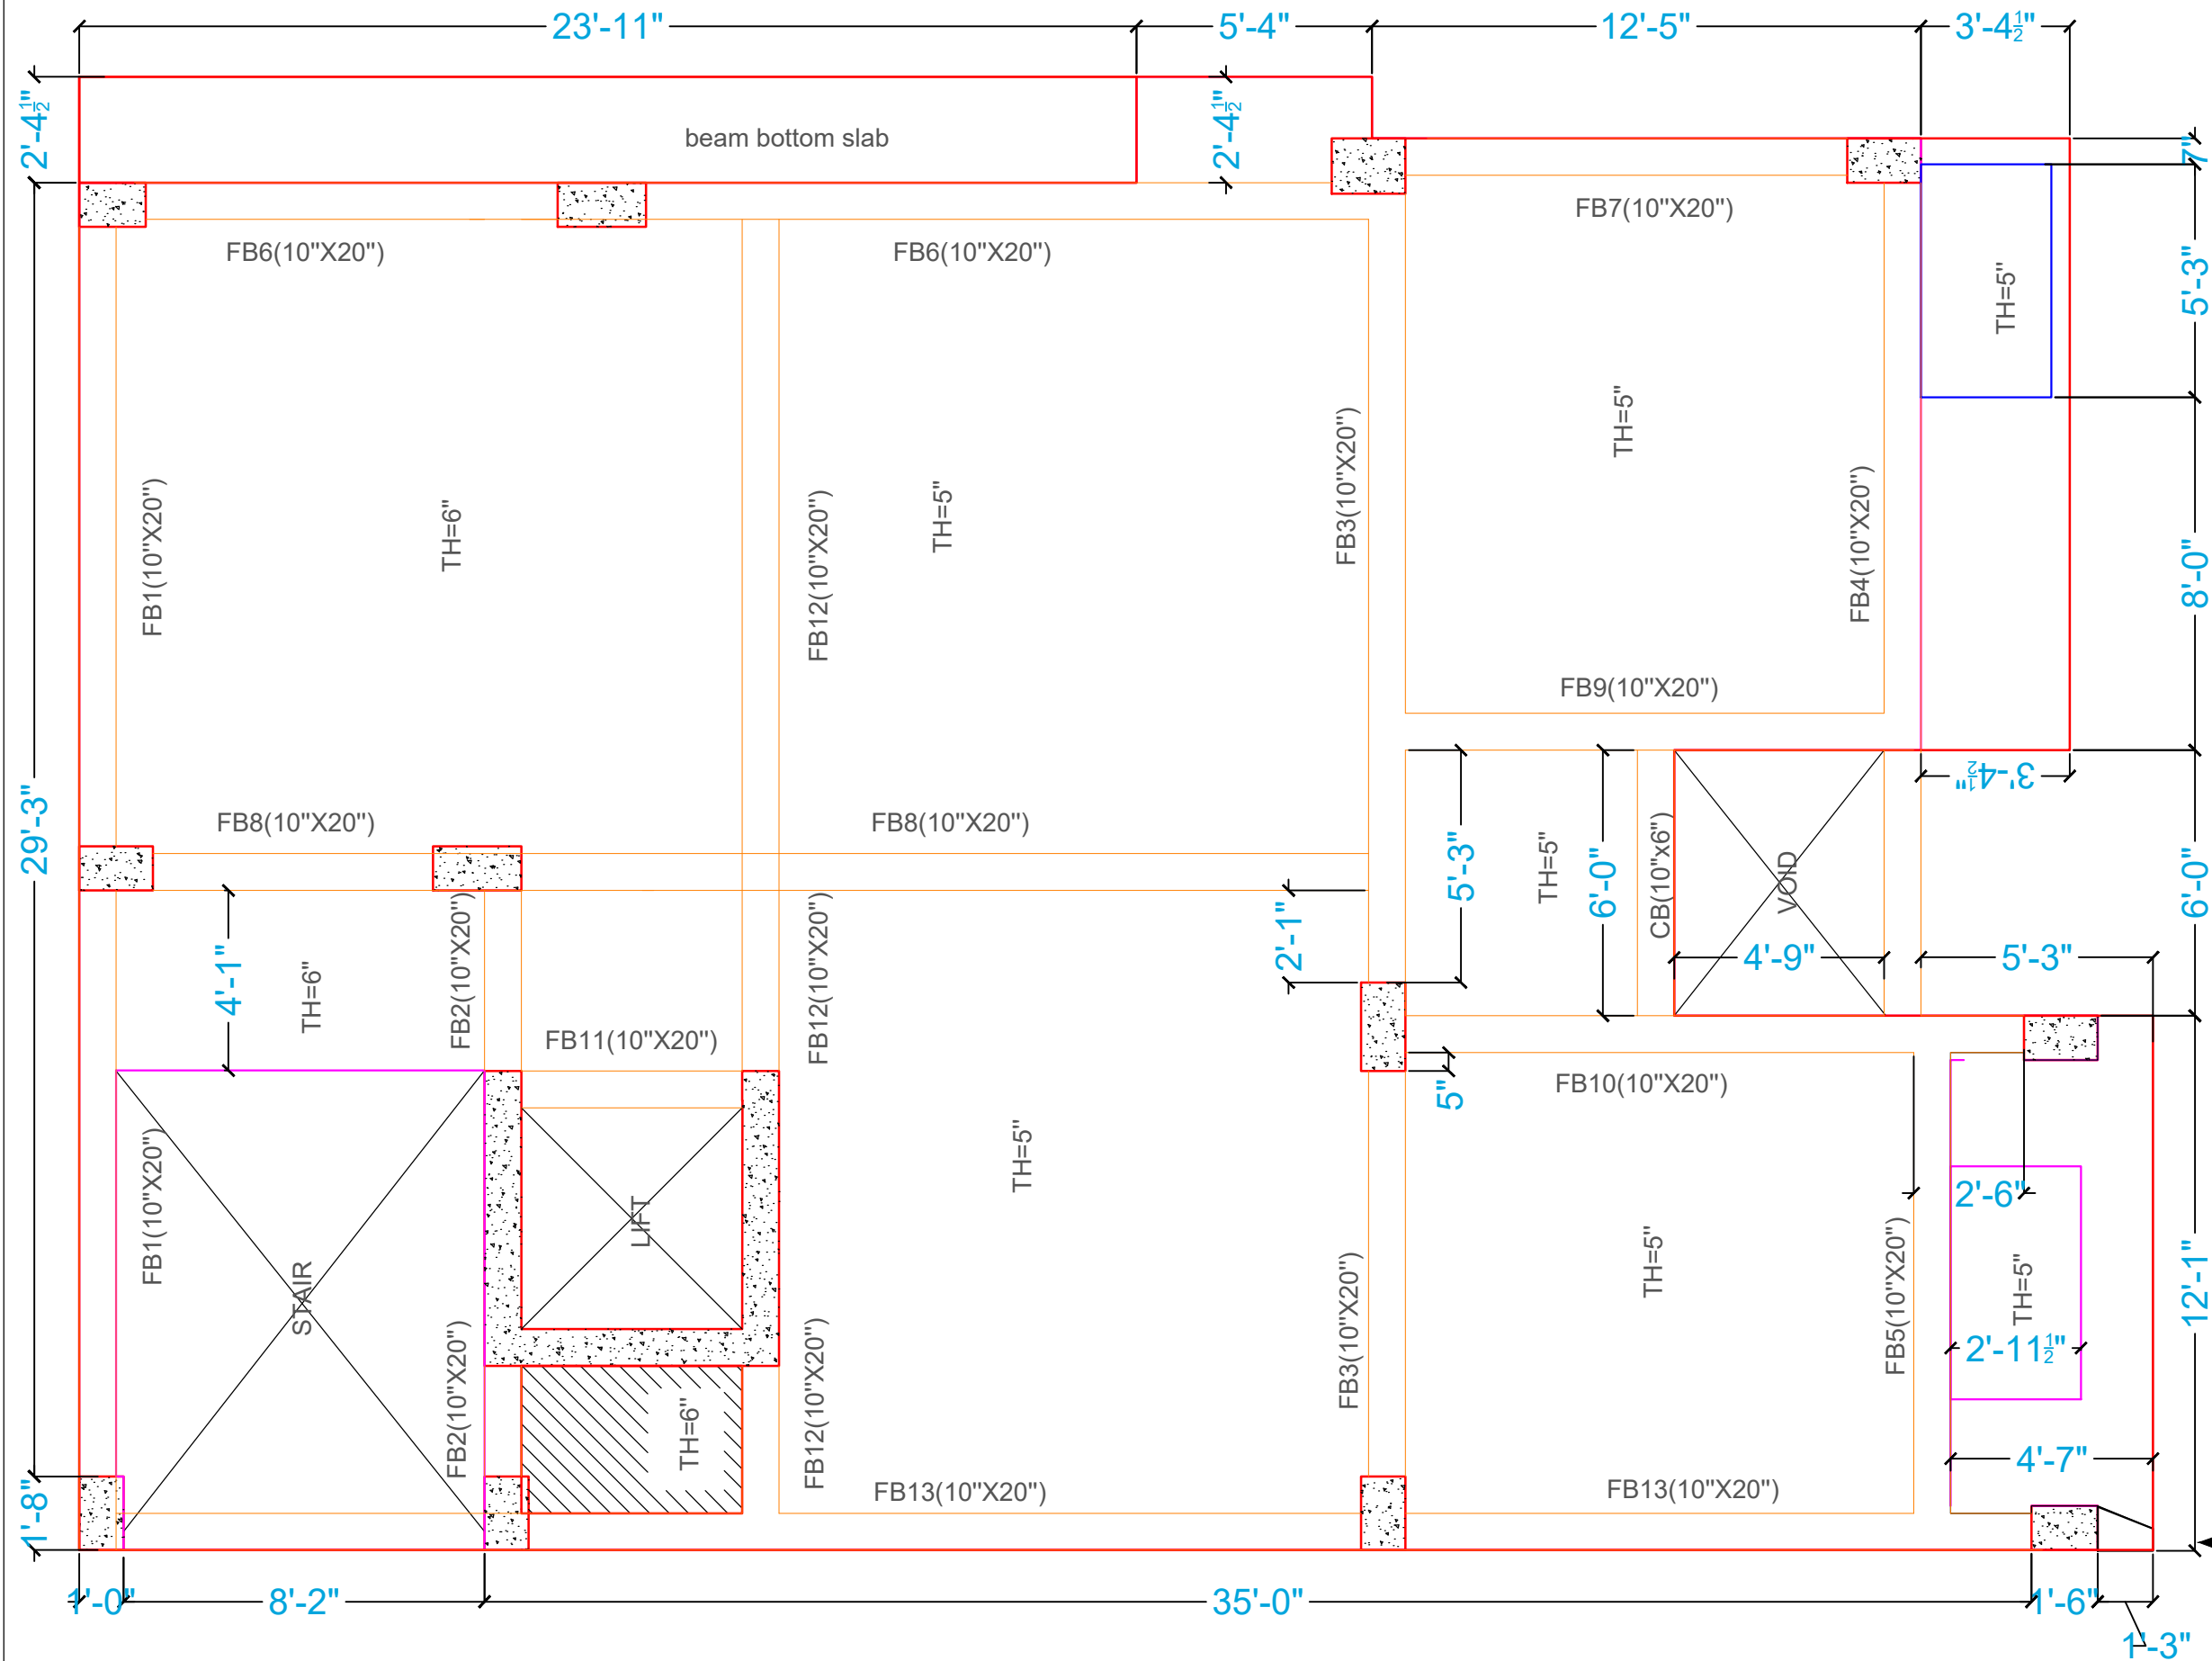

3 RD FLOOR ROOF BEAM LAYOUT PLAN
SCALE: 1:100

PROJECT
PROPOSED G+6= 07 (SEVEN) STORIED RESIDENTIAL BUILDING PLAN (TYPE A-A3) ON PLOT-9287, ROAD-12, BLOCK-N, BASUNDHARA RESIDENTIAL AREA, DHAKA.
CONSULTANT
EDIFICE CONSTRUCTION & CONSULTANTS H-62/5/E , Rupayan, P&F Square,Flat-6A & 6B North Sagufta,New Road Kalsbi,Dhaka-1216 E-mail:nuralam.edifice@gmail.com cell-01796585611,01685663316
OWNER/CLIENT
MAHAMUDAL HASSAN
ARCHITECT
AR. RAFIUL ISLAM RAFI B.ARCH(SUST)
CHECKED & APPROVED BY
ENGR. MD. NUR ALAM B.Sc. in CIVIL ENGG. FIEB-11295
DRAWN BY
MD. MOHAIMENUL ISLAM
DRAWING TITLE
STUCTURAL WORKING DRAWING
SHEET TITLE
3 RD FLOOR ROOF BEAM LAYOUT PLAN
SUBMISSION DATE:-
05.02.2026
SHEET NO:
A-02

PROJECT

PROPOSED G+6= 07 (SEVEN) STORIED RESIDENTIAL
BUILDING PLAN (TYPE A-A3) ON PLOT-9287,
ROAD-12, BLOCK-N, BASUNDHARA RESIDENTIAL
AREA, DHAKA.

CONSULTANT



EDIFICE CONSTRUCTION &
CONSULTANTS
H-62/5/E, Rupayan,
P&F Square, Flat-6A & 6B
North Sagufta, New Road
Kalshi, Dhaka-1216
E-mail: nuralam.edifice@gmail.com
cell-01796585611, 01685663316

OWNER/CLIENT

MAHAMUDAL HASSAN

ARCHITECT

AR. RAFIUL ISLAM RAFI
B.ARCH(SUST)

CHECKED &
APPROVED BY

ENGR. MD. NUR ALAM
B.Sc. in CIVIL ENGG.
FIEB-11295

DRAWN BY

MD. MOHAIMENUL ISLAM

DRAWING TITLE

STUCTURAL
WORKING DRAWING

SHEET TITLE


3 RD FLOOR ROOF
BEAM DETAILS

SUBMISSION DATE:-


05.02.2026

SHEET NO:


A-03

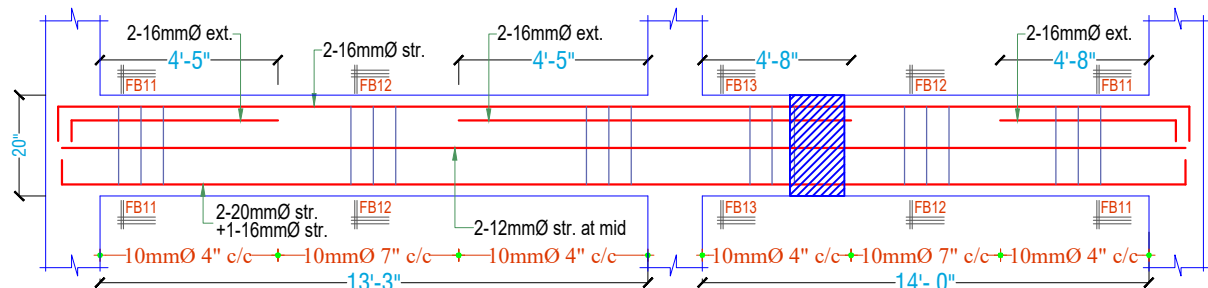


LONG SECTION OF FLOOR BEAM-1 (10"X20")

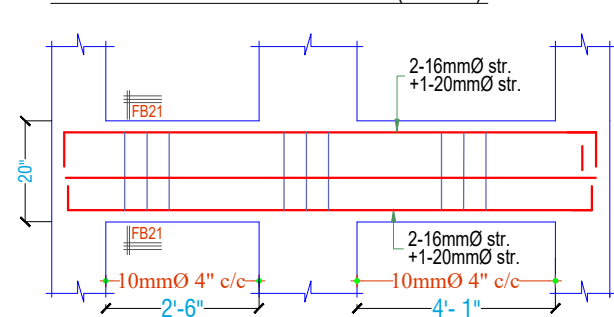


LONG SECTION OF FLOOR BEAM-2 (10"X20")

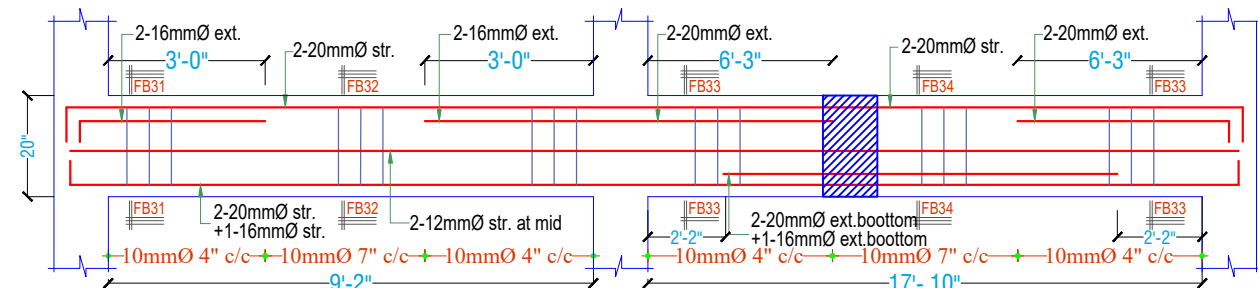


LONG SECTION OF FLOOR BEAM-3 (10"X20")

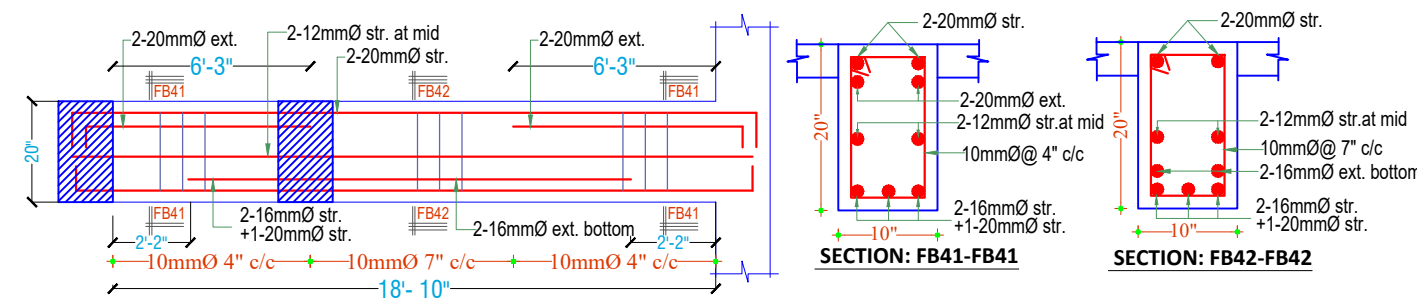


LONG SECTION OF FLOOR BEAM-4 (10"X20")

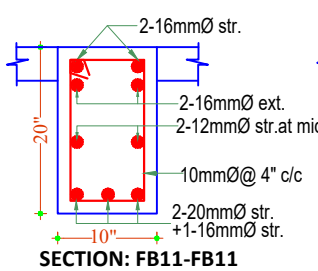


SECTION: FB11-FB11

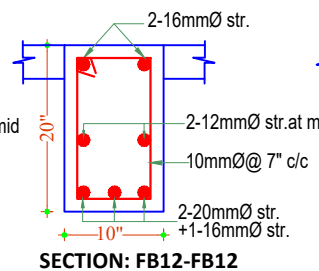


SECTION: FB12-FB12

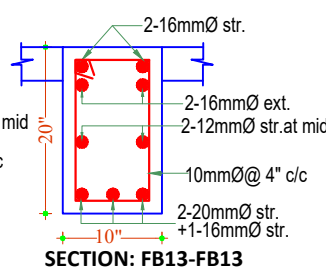


SECTION: FB13-FB13

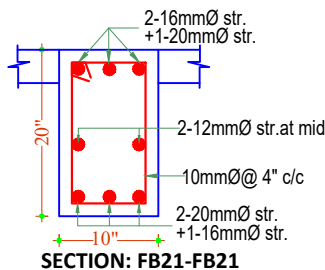


SECTION: FB21-FB21

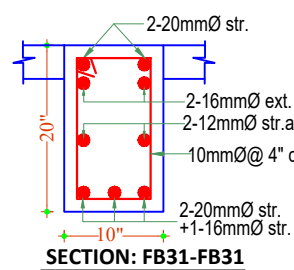


SECTION: FB31-FB31

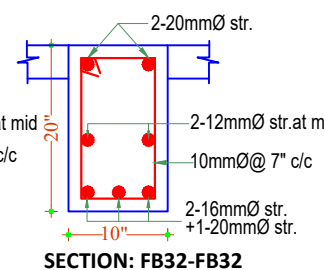


SECTION: FB32-FB32

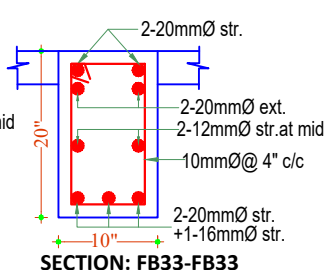


SECTION: FB33-FB33

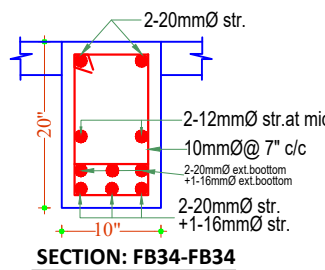



SECTION: FB34-FB34

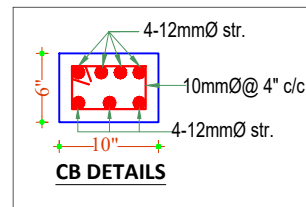



CB DETAILS

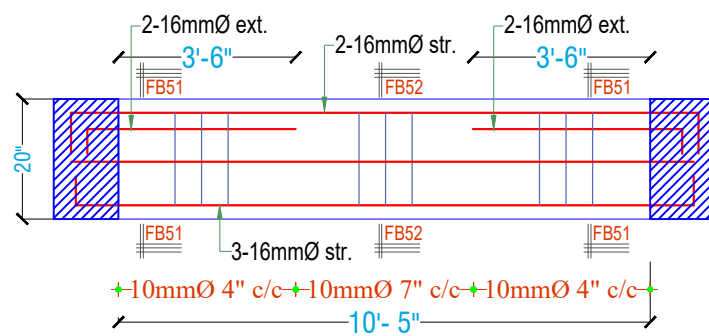



LONG SECTION OF FLOOR BEAM-5 (10"X20")

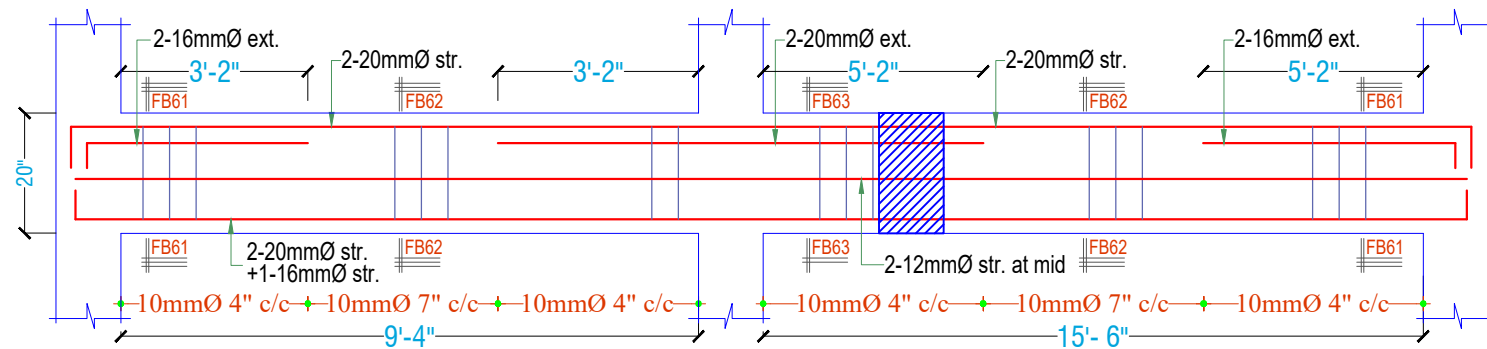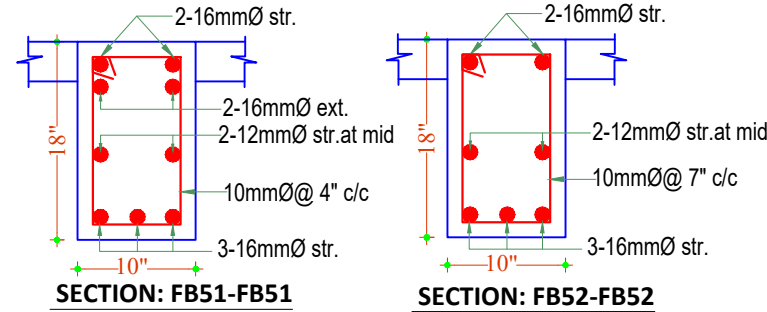


LONG SECTION OF FLOOR BEAM-6 (10"X20")

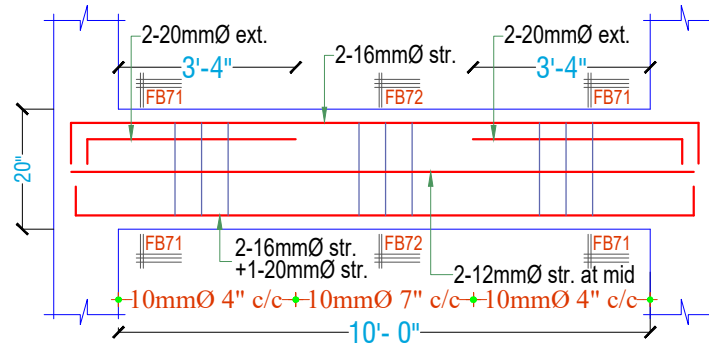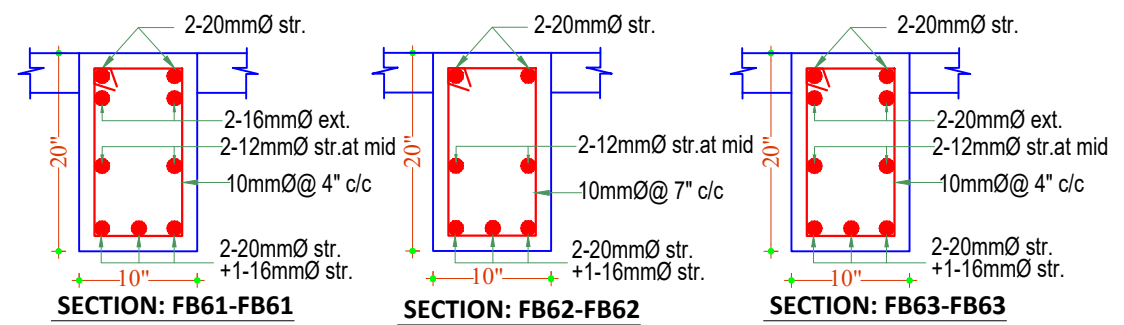


LONG SECTION OF FLOOR BEAM-7 (10"X20")

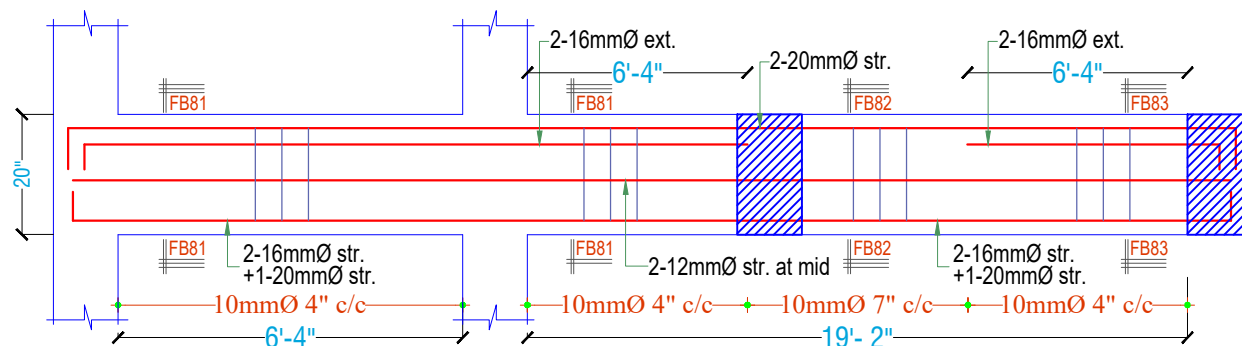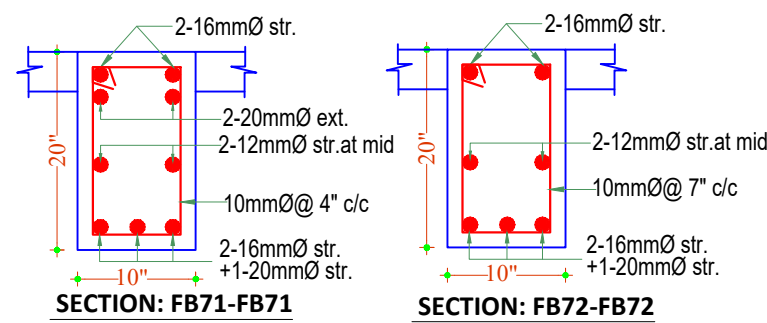


LONG SECTION OF FLOOR BEAM-8 (10"X20")

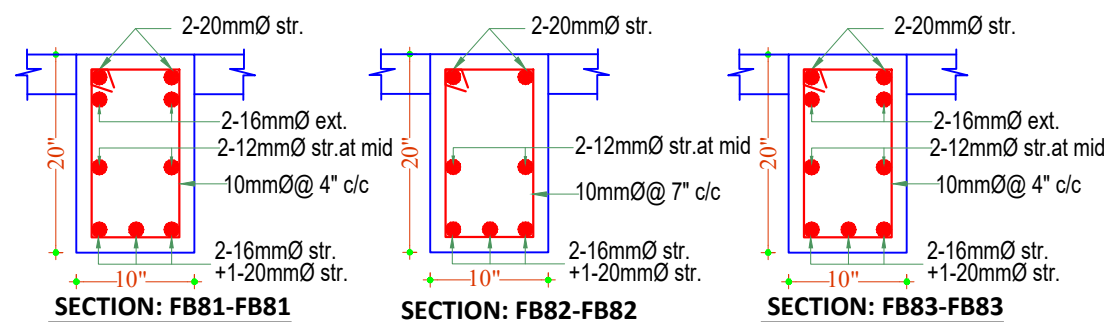


PROJECT PROPOSED G+6= 07 (SEVEN) STORED RESIDENTIAL BUILDING PLAN (TYPE A-A3) ON PLOT-9287, ROAD-12, BLOCK-N, BASUNDHARA RESIDENTIAL AREA, DHAKA.
CONSULTANT  EDIFICE CONSTRUCTION & CONSULTANTS H-62/5/E, Rupayan, P&F Square, Flat-6A & 6B North Sagufta, New Road Kalshi, Dhaka-1216 E-mail: nuralam.edifice@gmail.com cell-01796585611, 01685663316
OWNER/CLIENT MAHAMUDAL HASSAN
ARCHITECT AR. RAFIUL ISLAM RAFI B.ARCH(SUST)
CHECKED & APPROVED BY ENGR. MD. NUR ALAM B.Sc. in CIVIL ENGG. FIEB-11295
DRAWN BY MD. MOHAIMENUL ISLAM
DRAWING TITLE STUCTURAL WORKING DRAWING
SHEET TITLE 3 RD FLOOR ROOF BEAM DETAILS
SUBMISSION DATE:- 05.02.2026
SHEET NO: A-04

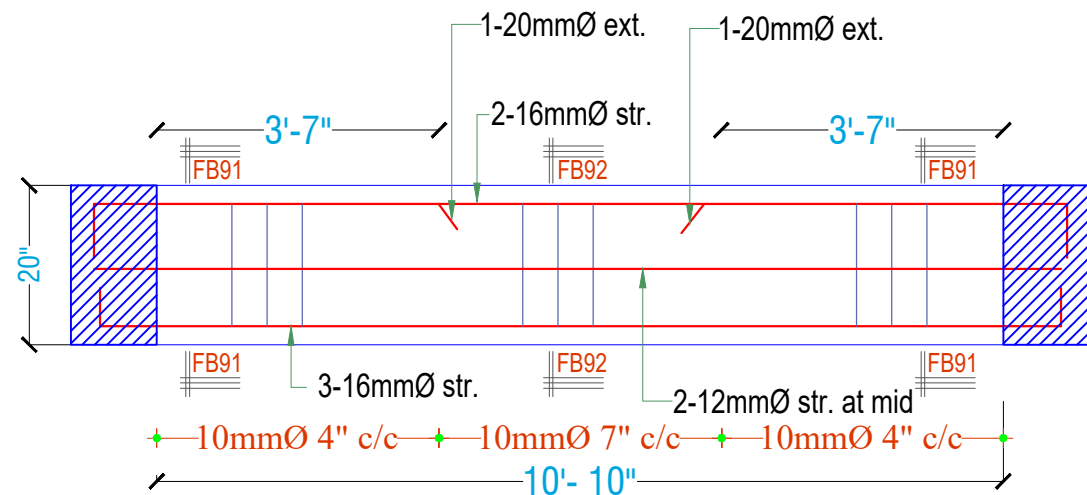


LONG SECTION OF FLOOR BEAM-09 (10"X20")

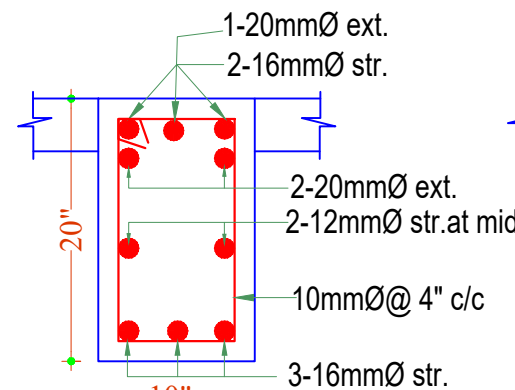


SECTION: FB91-FB91

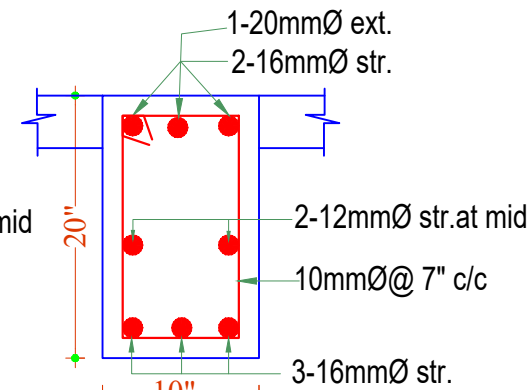


SECTION: FB92-FB92

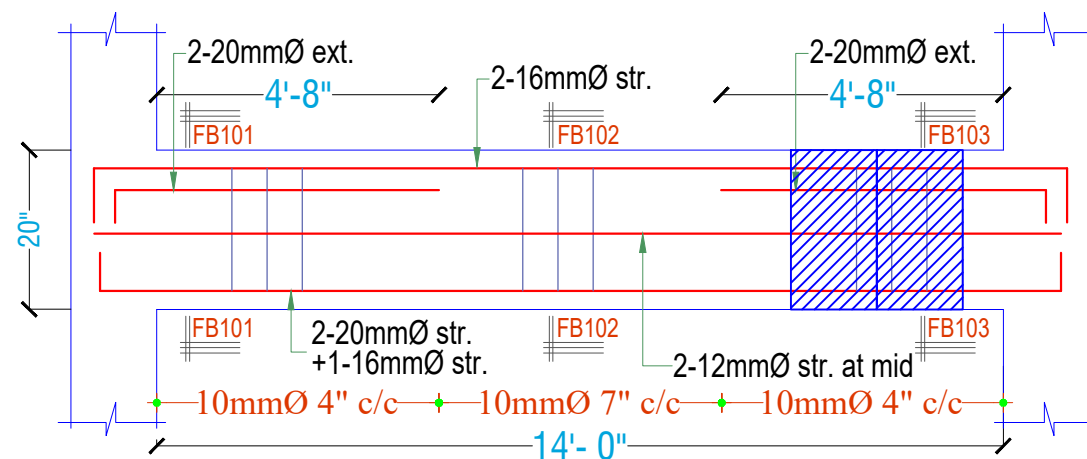


LONG SECTION OF FLOOR BEAM-10 (10"X20")

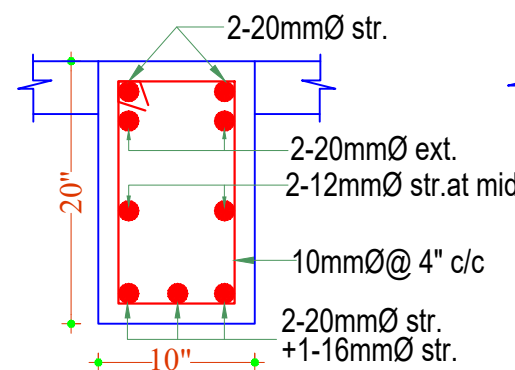


SECTION: FB101-FB101

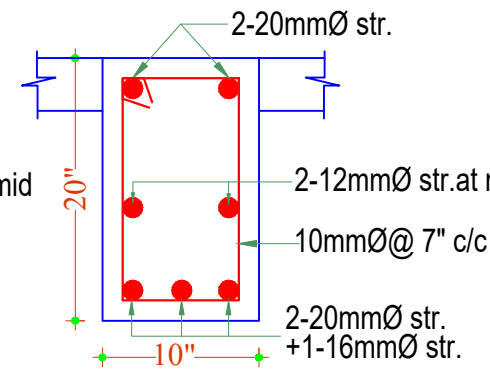


SECTION: FB102-FB102

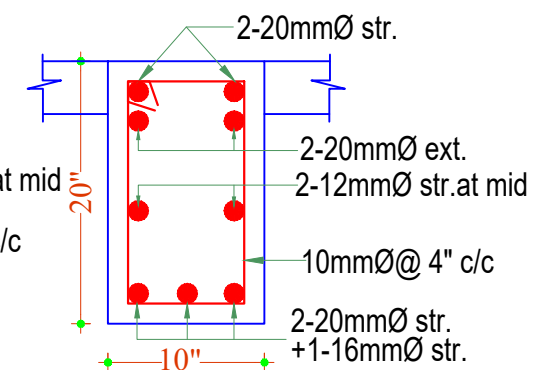

SECTION: FB103-FB103

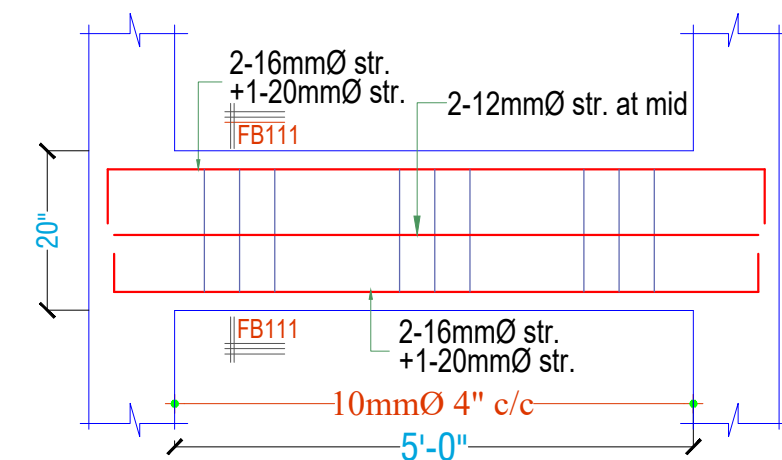

LONG SECTION OF FLOOR BEAM-11 (10"X20")

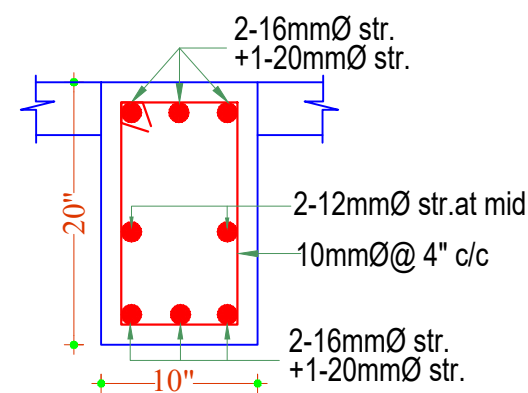

SECTION: FB111-FB111

PROJECT

PROPOSED G+6-07 (SEVEN) STORED RESIDENTIAL BUILDING PLAN (TYPE A-A3) ON PLOT-9287, ROAD-12, BLOCK-N, BASUNDHARA RESIDENTIAL AREA, DHAKA.

CONSULTANT



EDIFICE CONSTRUCTION & CONSULTANTS
H-62/5/E, Rupayan,
P&F Square, Flat-6A & 6B
North Sagufta, New Road
Kalshi, Dhaka-1216
E-mail: nuralam.edifice@gmail.com
cell-01796585611, 01685663316

OWNER/CLIENT

MAHAMUDAL HASSAN

ARCHITECT

AR. RAFIUL ISLAM RAFI
B.ARCH(SUST)

CHECKED & APPROVED BY

ENGR. MD. NUR ALAM
B.Sc. in CIVIL ENGG.
FIEB-11295

DRAWN BY

MD. MOHAIMENUL ISLAM

DRAWING TITLE

STUCTURAL
WORKING DRAWING

SHEET TITLE

3 RD FLOOR ROOF
BEAM DETAILS

SUBMISSION DATE:-

05.02.2026

SHEET NO:

A-05

PROJECT

PROPOSED G+6= 07 (SEVEN) STORIED RESIDENTIAL
BUILDING PLAN (TYPE A-A3) ON PLOT-9287,
ROAD-12, BLOCK-N, BASUNDHARA RESIDENTIAL
AREA, DHAKA.

CONSULTANT



EDIFICE CONSTRUCTION &
CONSULTANTS
H-62/5/E, Rupayan,
P&F Square, Flat-6A & 6B
North Sagutta, New Road
Kalshi, Dhaka-1216
E-mail: nuralam.edifice@gmail.com
cell-01796585611, 01685663316

OWNER/CLIENT

MAHAMUDAL HASSAN

ARCHITECT

AR. RAFIUL ISLAM RAFI
B.ARCH(SUST)

CHECKED &
APPROVED BY

ENGR. MD. NUR ALAM
B.Sc. in CIVIL ENGG.
FIEB-11295

DRAWN BY

MD. MOHAIMENUL ISLAM

DRAWING TITLE

STUCTURAL
WORKING DRAWING

SHEET TITLE


3 RD FLOOR ROOF
BEAM DETAILS

SUBMISSION DATE:-


05.02.2026

SHEET NO:


A-06

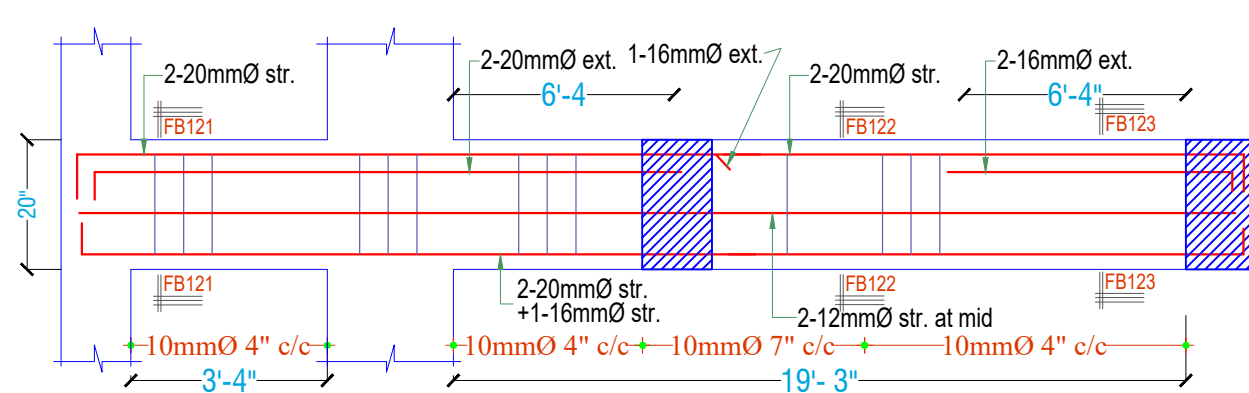


LONG SECTION OF FLOOR BEAM-12 (10"X20")

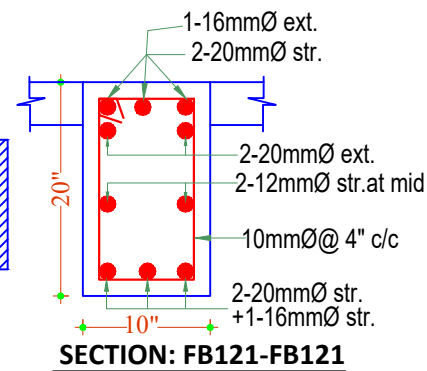


SECTION: FB121-FB121

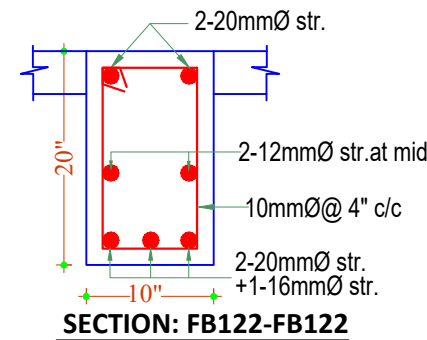


SECTION: FB122-FB122

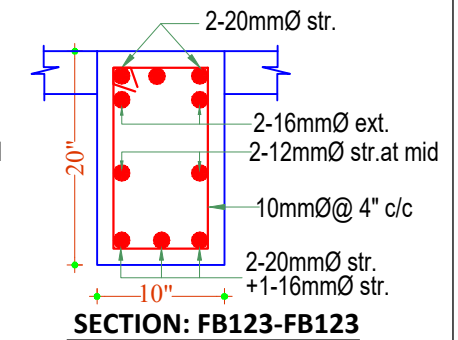


SECTION: FB123-FB123

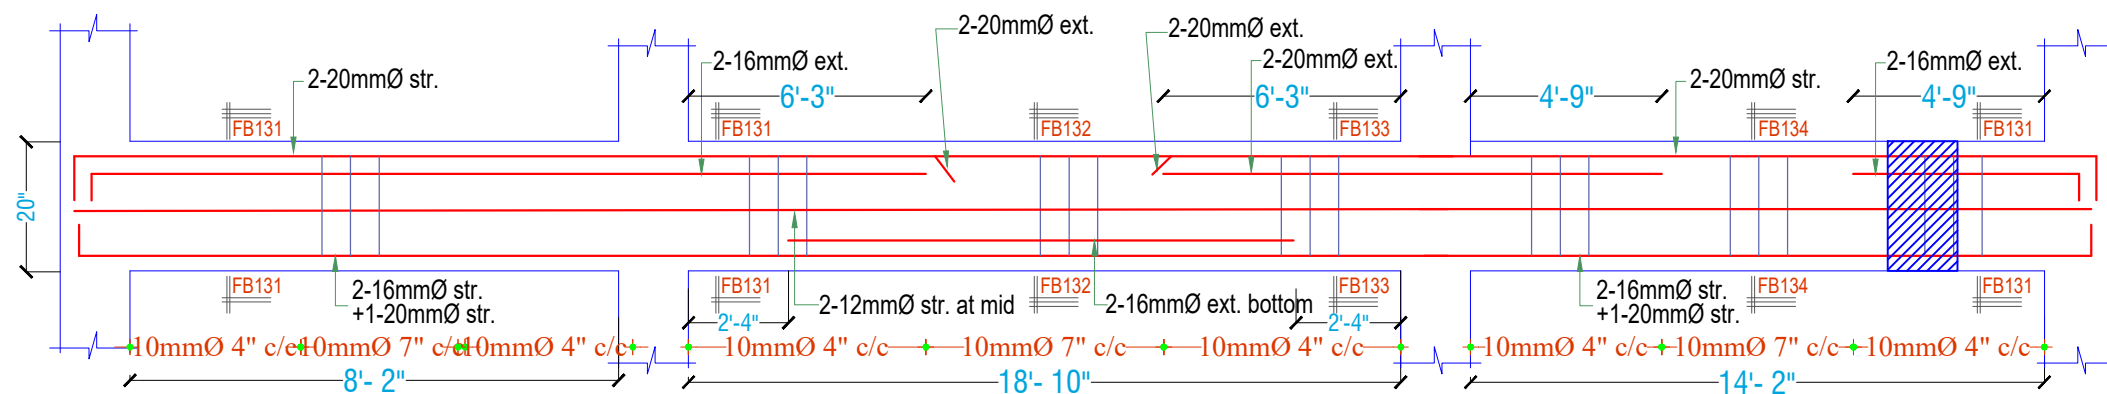


LONG SECTION OF FLOOR BEAM-13 (10"X20")

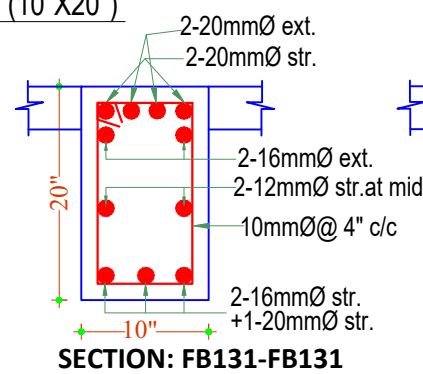


SECTION: FB131-FB131

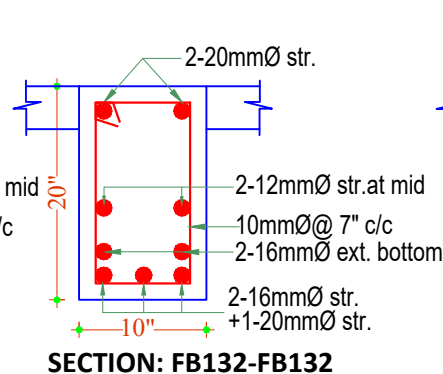



SECTION: FB132-FB132

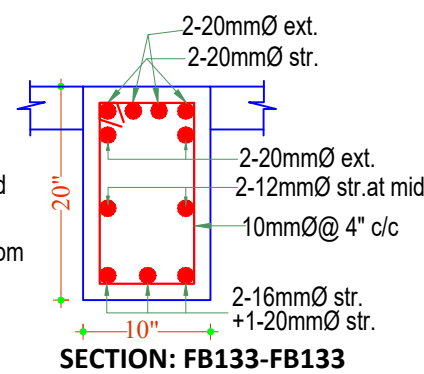

SECTION: FB133-FB133

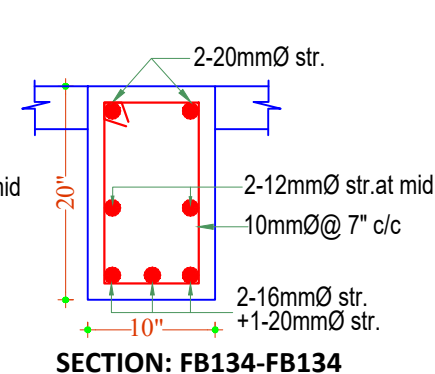

SECTION: FB134-FB134

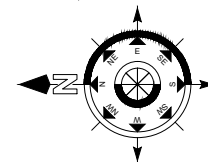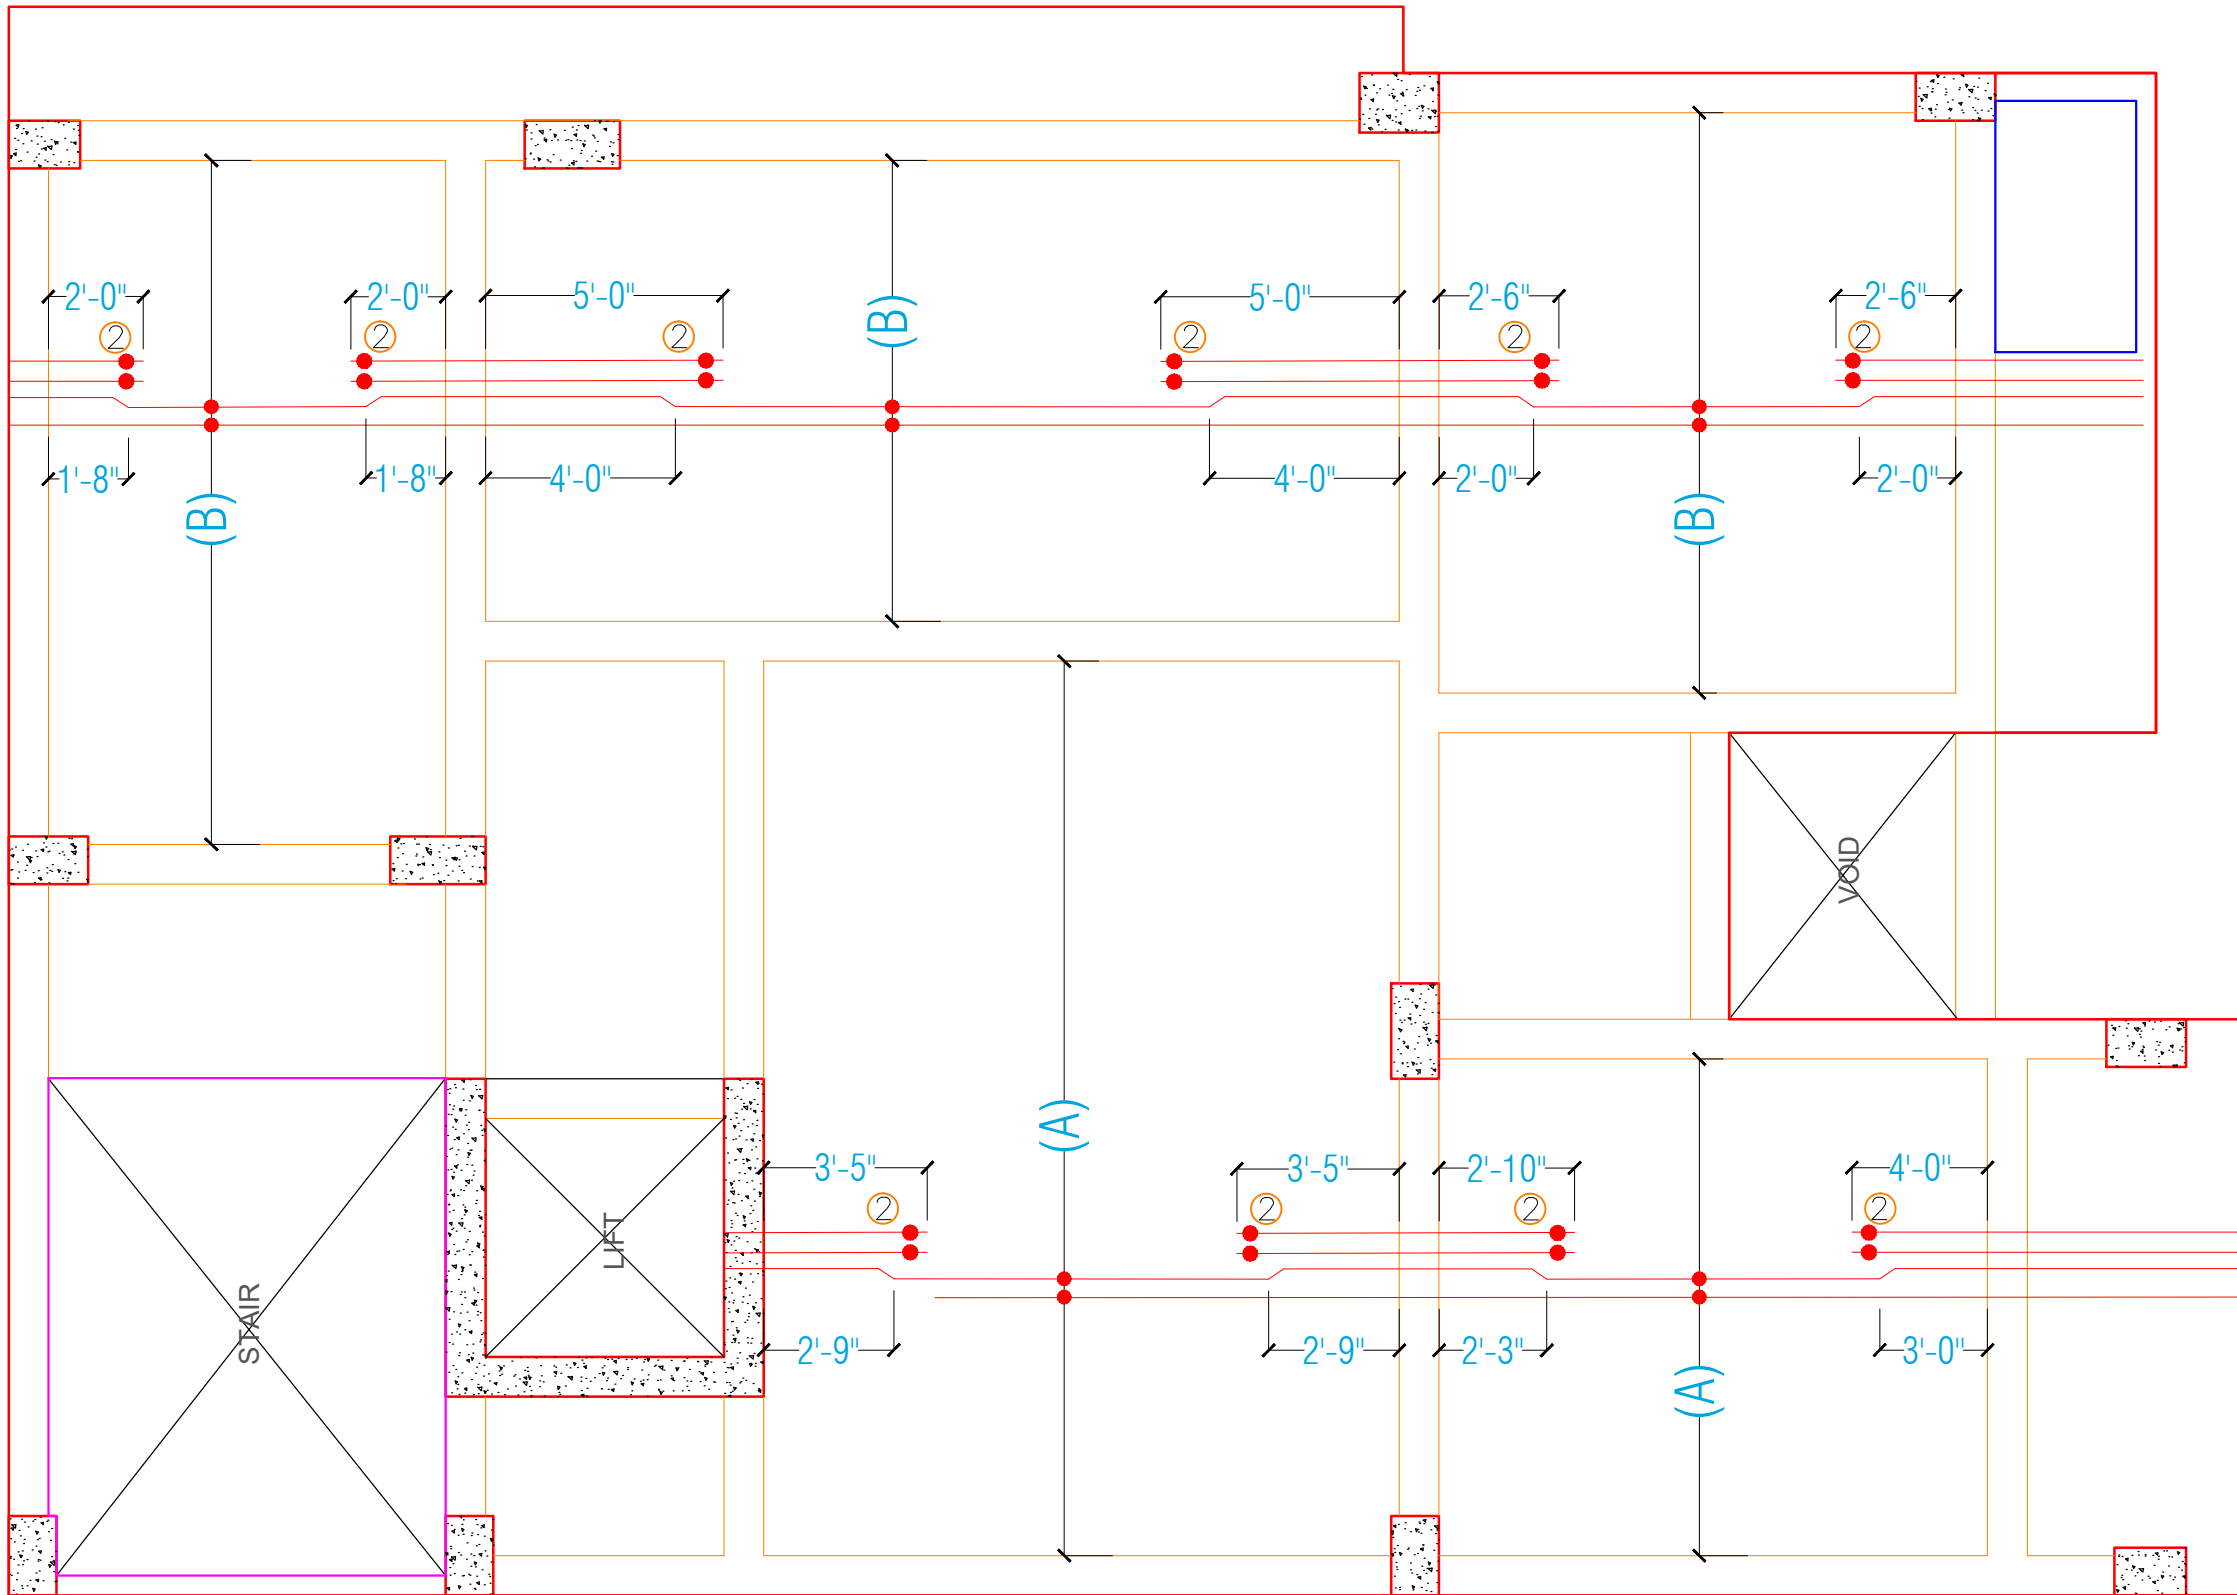

3 RD FLOOR ROOF SLAB REINFORCEMENT(N-S DIR.)
SCALE: 1:100

LEGEND

Binder
A= Ø10mm @ 6.5" C/C
B= Ø10mm @ 7"C/C
1=1-10Ø ext.top
2= 2-10Ø ext.top

PROJECT

PROPOSED G+6= 07 (SEVEN) STORED RESIDENTIAL
BUILDING PLAN (TYPE A-A3) ON PLOT-9287,
ROAD-12, BLOCK-N, BASUNDHARA RESIDENTIAL
AREA, DHAKA.

CONSULTANT



EDIFICE CONSTRUCTION &
CONSULTANTS
H-62/5/E , Rupayan,
P&F Square.Flat-6A & 6B
North Sagufta,New Road
Kalshi,Dhaka-1216
E-mail:nuralam.edifice@gmail.com
cell-01796585611,01685663316

OWNER/CLIENT

MAHAMUDAL HASSAN

ARCHITECT

AR. RAFIUL ISLAM RAFI
B.ARCH(SUST)

CHECKED & APPROVED BY

ENGR. MD. NUR ALAM
B.Sc. in CIVIL ENGG.
FIEB-11295

DRAWN BY

MD. MOHAIMENUL ISLAM

DRAWING TITLE

STUCTURAL
WORKING DRAWING

SHEET TITLE


3RD FLOOR ROOF SLAB
REINFORCEMENT(N-S DIR)

SUBMISSION DATE:-

05.02.2026

SHEET NO:

A-08

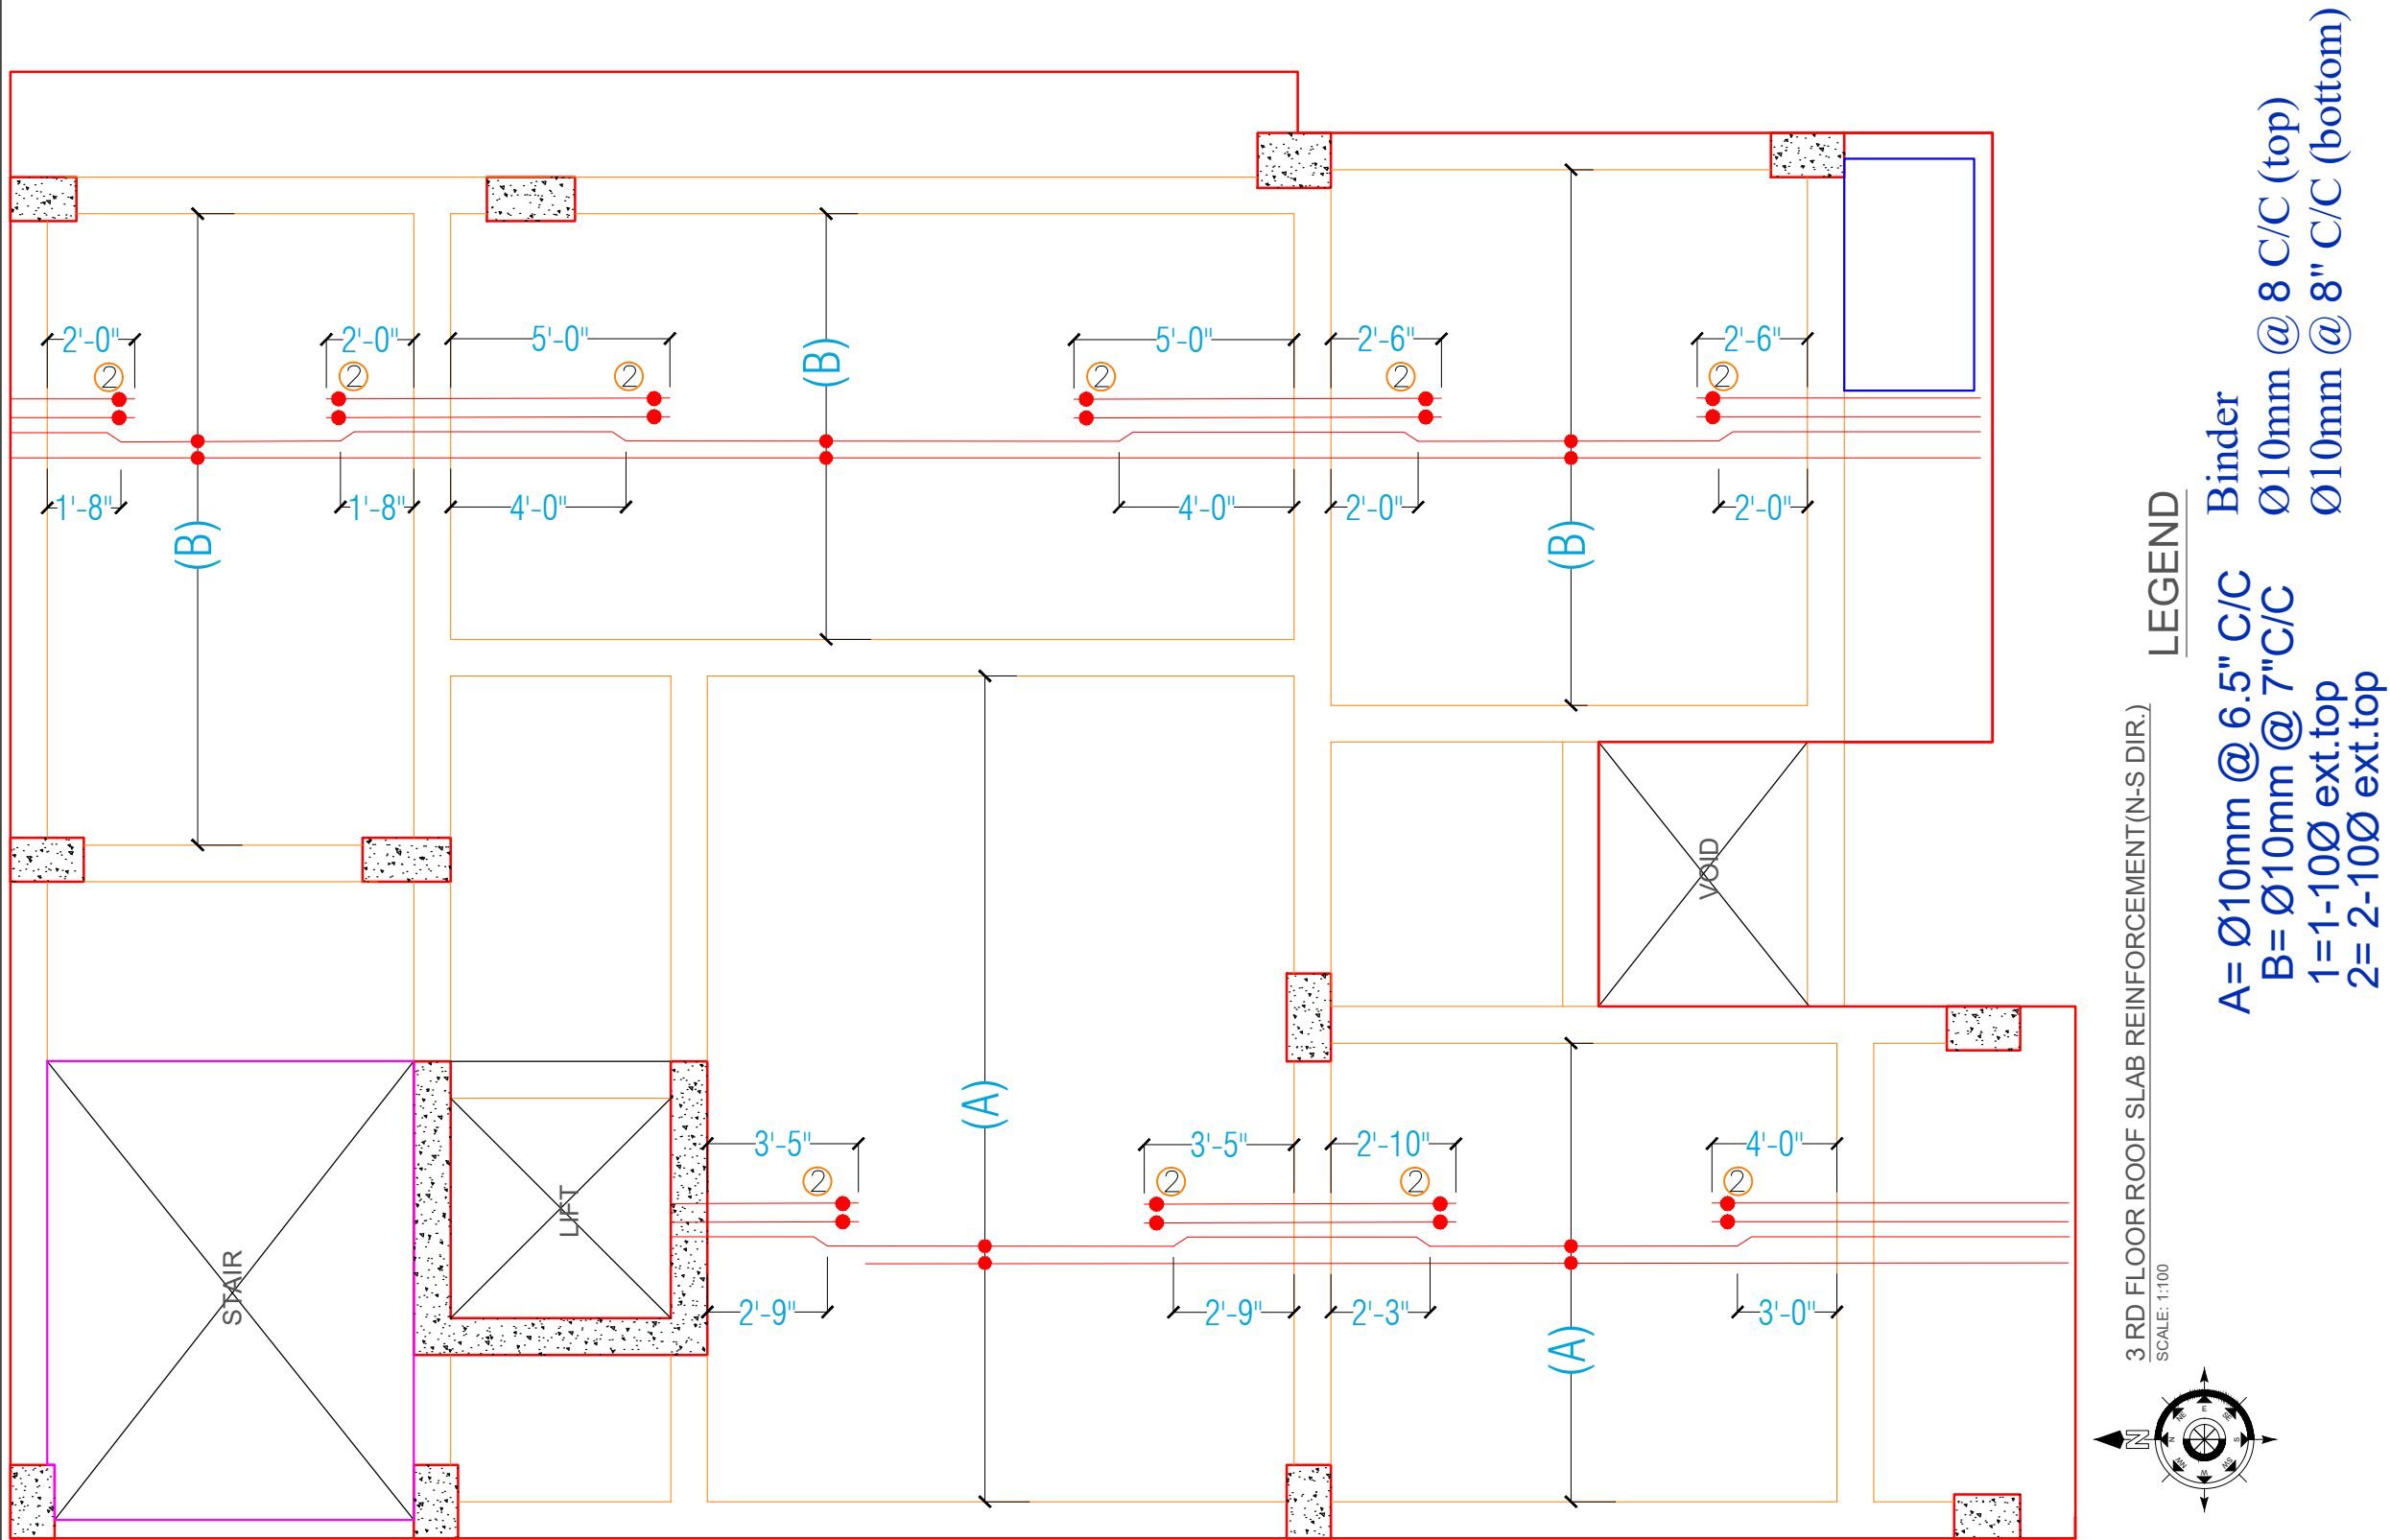

LEGEND

A= Ø10mm @ 6.5" C/C
B= Ø10mm @ 7" C/C
1= 1-10Ø ext.top
2= 2-10Ø ext.top

Binder
Ø10mm @ 8 C/C (top)
Ø10mm @ 8" C/C (bottom)

PROJECT

PROPOSED G+6= 07 (SEVEN) STORIED RESIDENTIAL
BUILDING PLAN (TYPE A-A3) ON PLOT-9287,
ROAD-12, BLOCK-N, BASUNDHARA RESIDENTIAL
AREA, DHAKA.

CONSULTANT



EDIFICE CONSTRUCTION &
CONSULTANTS
H-62/5/E, Rupayan,
P&F Square, Flat-6A & 6B
North Sagufta, New Road
Kalshi, Dhaka-1216
E-mail: nuralam.edifice@gmail.com
cell-01796585611, 01685663316

OWNER/CLIENT

MAHAMUDAL HASSAN

ARCHITECT

AR. RAFIUL ISLAM RAFI
B.ARCH(SUST)

CHECKED & APPROVED BY

ENGR. MD. NUR ALAM
B.Sc. in CIVIL ENGG.
FIEB-11295

DRAWN BY

MD. MOHAIMENUL ISLAM

DRAWING TITLE

STUCTURAL
WORKING DRAWING

SHEET TITLE

3RD FLOOR ROOF SLAB
REINFORCEMENT(N-S DIR.)

SUBMISSION DATE:-

05.02.2026

SHEET NO:

A-08